

& Friction

Architecture operating as a spatial device
— twisting spatial flows and mediating urban interaction through multisensory networks.

Between Flow &

Architectural Portfolio | Selected Works | 2023 - 2025
SEHYUN KIM



CV

SEHYUN KIM

2000.09.28

Seoul, Republic of Korea

Phone : +82 10 3747 4371

Email : sehyun20@icloud.com

Language. Korean (native) English (fluent)

Education. Kookmin University, Seoul, Republic of Korea
Department of Architecture, Mar 2020-
4th year BArch student on leave

Experience. UAUS (Union of Architecture University Students)
2025.06 - 2025.10

Rural Volunteer work
2025.06 - 2025.07

Group leader of Samoonan Church, Youth Ministry
2025.01 - 2025.12

Rural Architectural Volunteer work
2024.06 - 2024.07

Architectural Research Society
2023.03 - 2025.06

Korea Airforce ATC (Air Traffic Control)
2021.02 - 2022.10

Software. Rhinoceros 8 Sketchup Revit
Photoshop Illustrator Indesign
Grasshopper Enscape D5 Render
Autocad Excel Powerpoint

Award. UAUS Competition
2025 / Excellence Prize(3rd Prize), Citizen Choice Prize

Design Excellence Scholarship
2025 / 7th 8th Architecture Studio

Future Church Contest
2023 / Bronze Prize

Dokdo Guest House Contest
2020 / Awarding

Contents.

1. Context Break Off
Urban Machinery



2. Floating Ground
Middle School



3. Museum is Moving
Museum Renovation



4. Art Path House
Housing




5. Future Church
Religious park



6. Symbiont
Pavilion Project




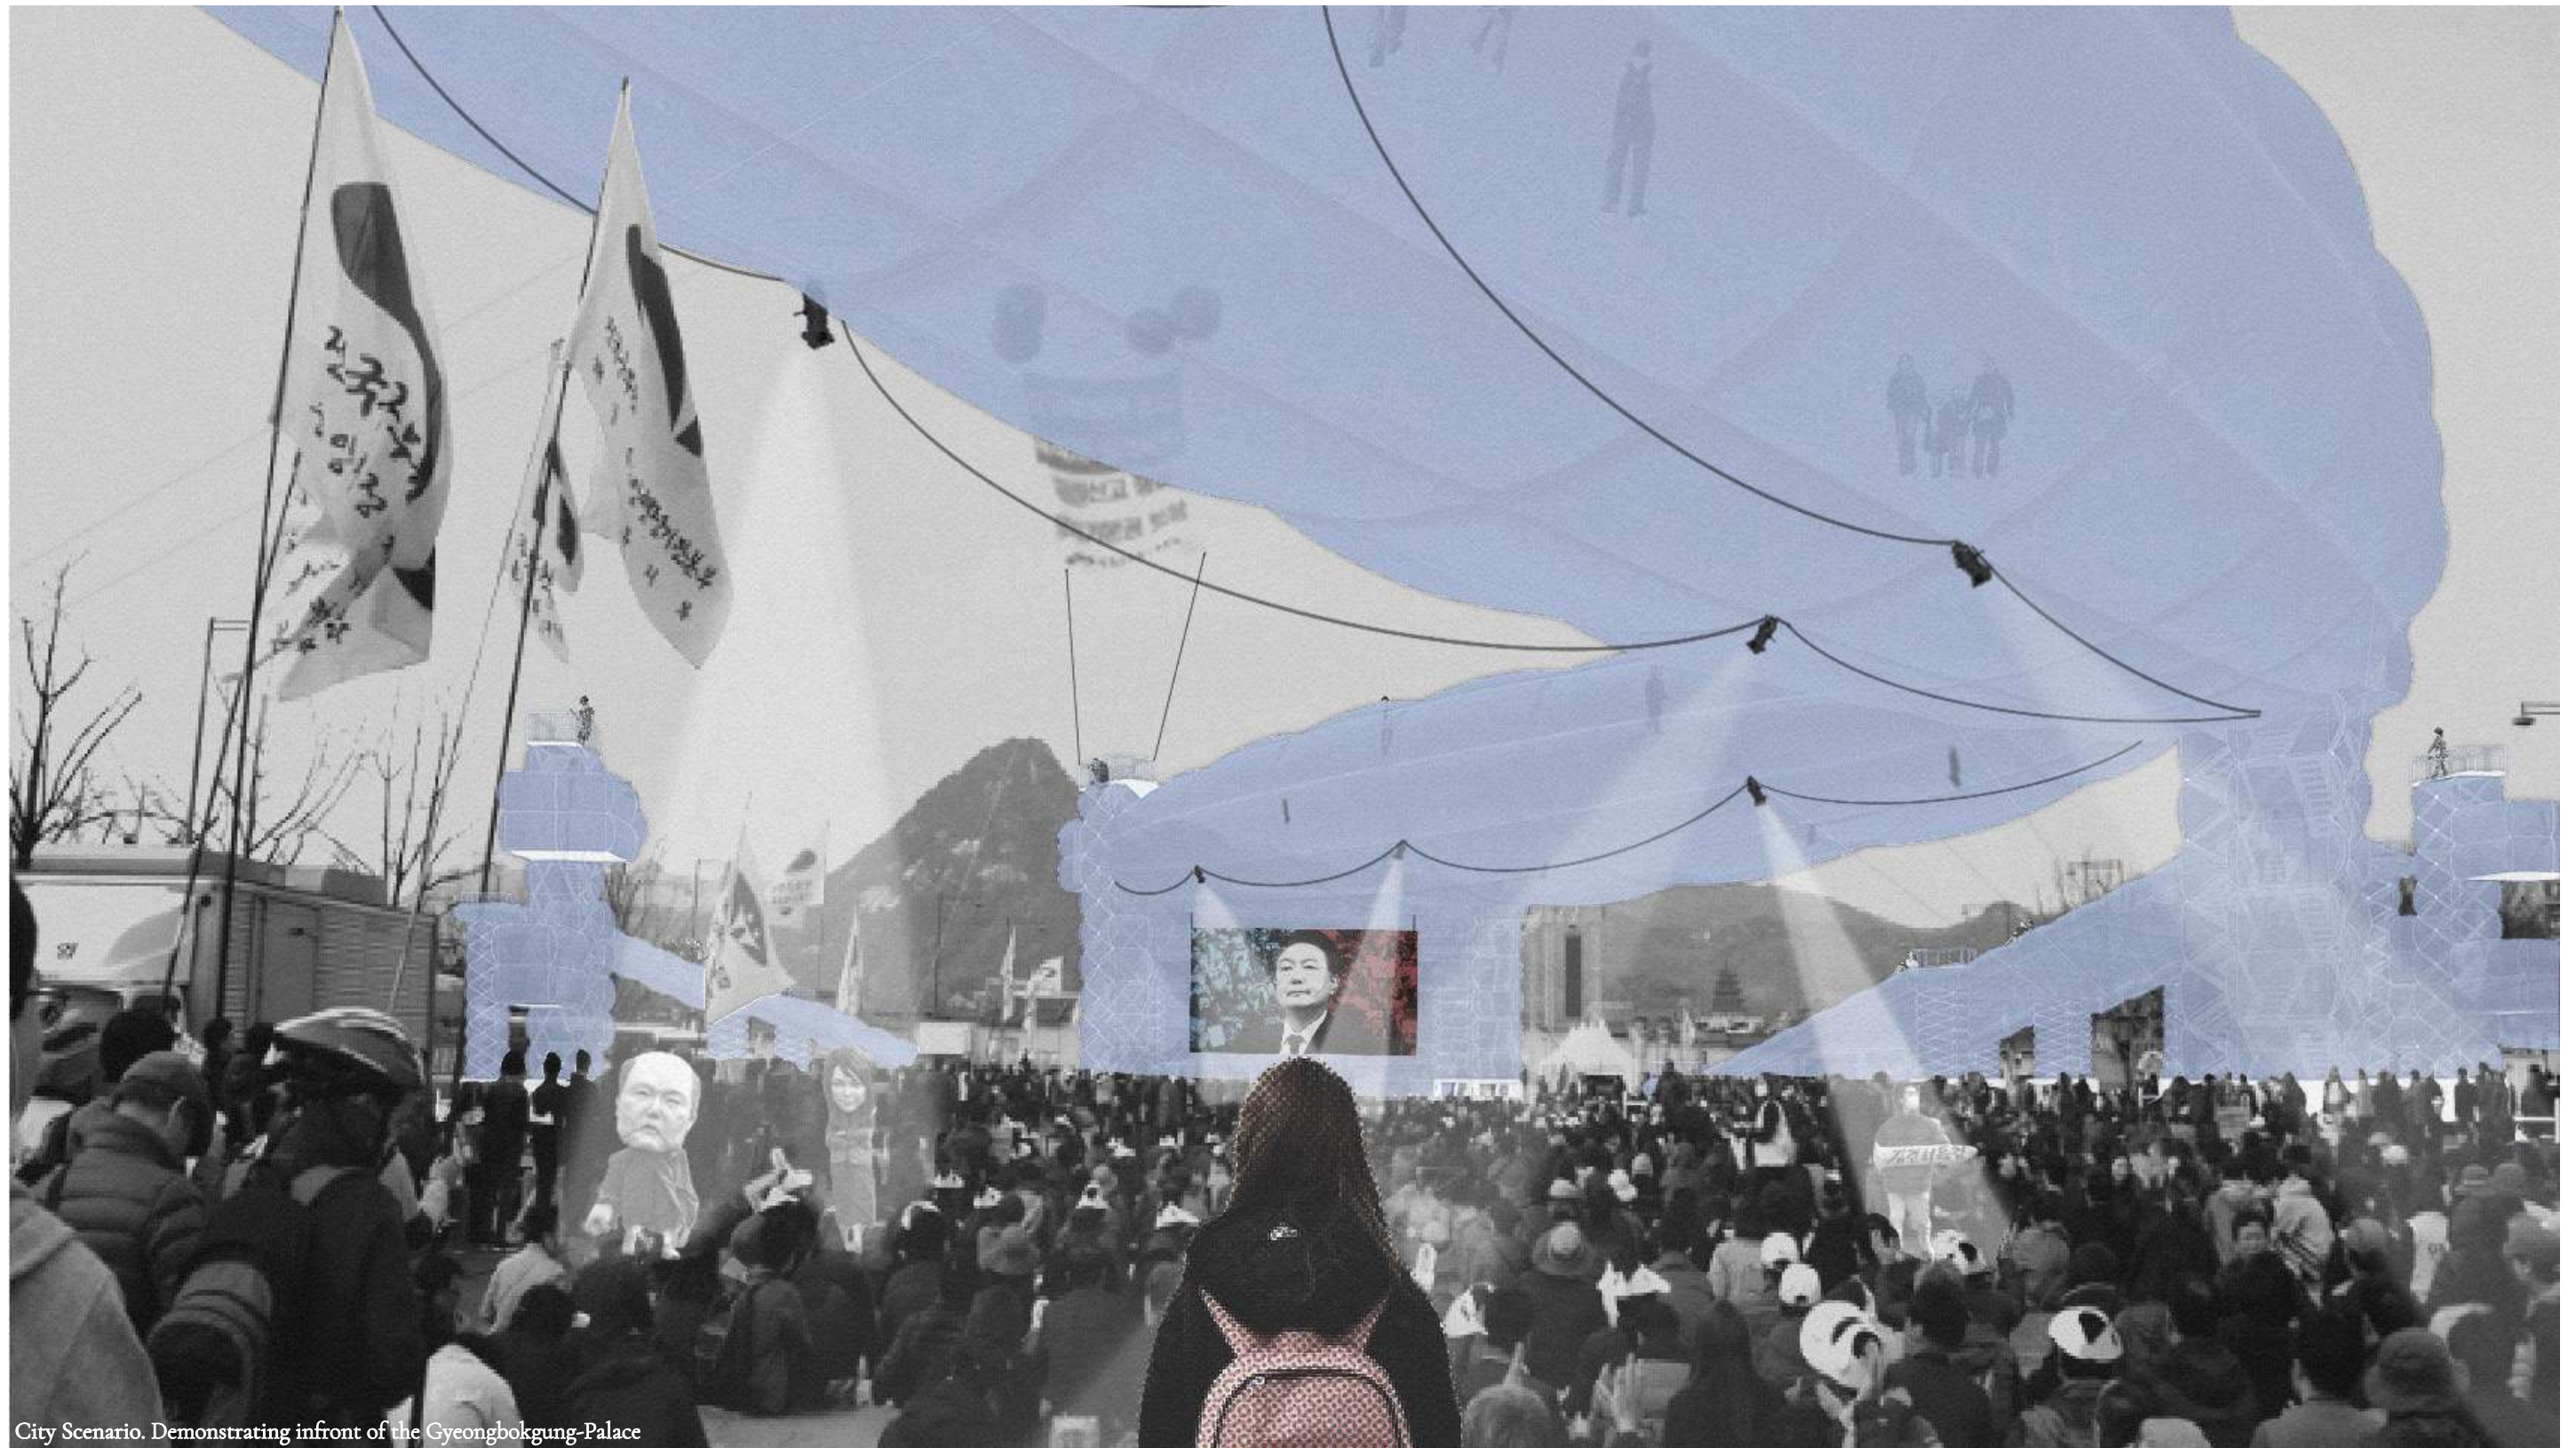

City Scenario. Demonstrating in front of the Gyeongbokgung-Palace

01 CONTEXT BREAK OFF

의도적 맥락끊기

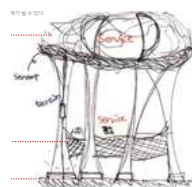


Project Information.

- Location : Gwangwhamun, Seoul
- Year : 2025 - 01
- Status : Academic thesis project (Individual)
- Type : Urban Machinery
- Instructor : Park Hee Chan

Prologue.

In the contemporary era, we increasingly encounter a breakdown in dialogue, accompanied by a tendency toward rigid, binary modes of thinking. Individuals often regard their own positions as entirely correct, thereby perceiving differing viewpoints not as alternatives, but as fundamentally “wrong.” Within this context of political conflict and social fragmentation, an important question arises: what role can religion play? This project originates from this inquiry and seeks to propose a spatial response from an urban perspective. It starts from 3 questions.

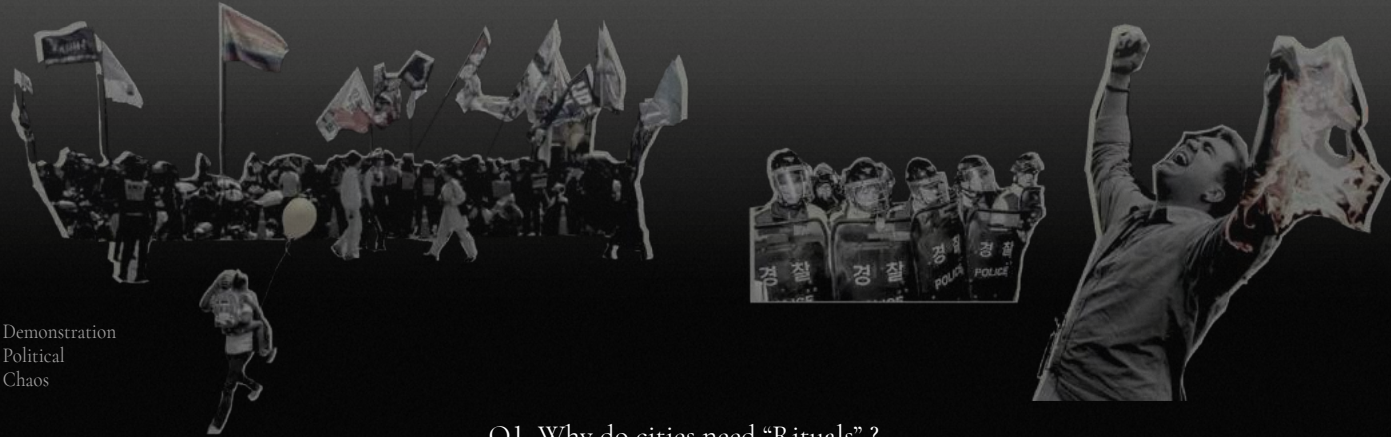


Demonstration
Political
Chaos

Q1. Why do cities need “Rituals” ?




Q2. How can we minimize conflict on Sejong-daero ?

Q3. Could the Architecture intervene these phenomena ?


Gwangwhamun, Sejeong-daero Road

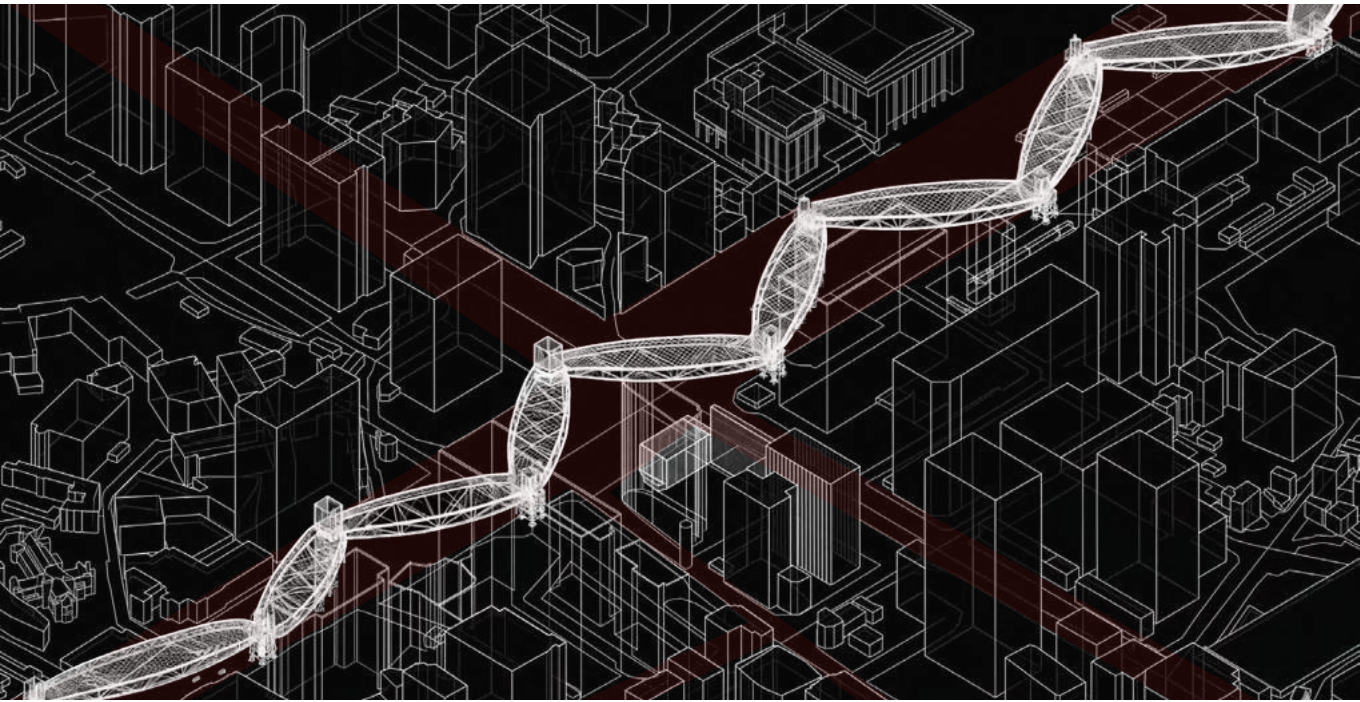

“ Break off Intentionally ”

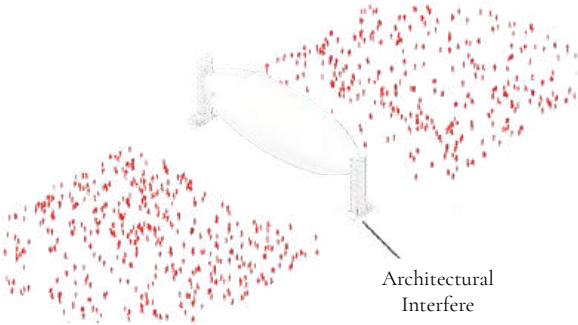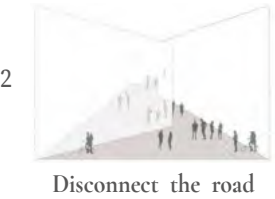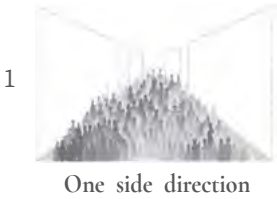

Architectural Interfere

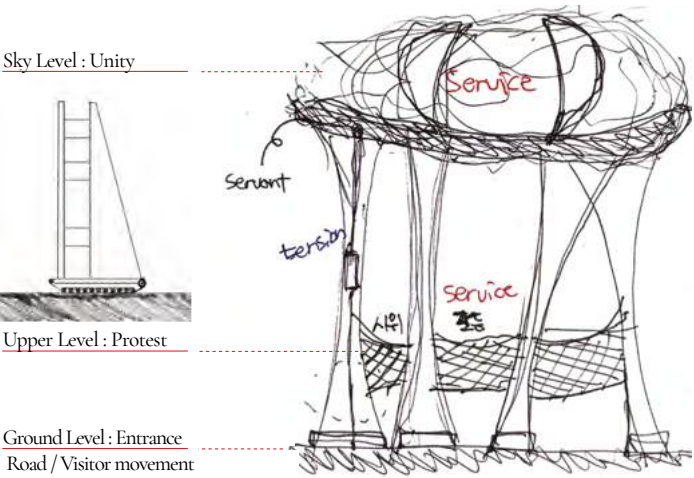

‘Inflated Vehicle’ IDEA Sketch
Membrane structure

A wall made of large air-filled membranes goes beyond a simple boundary, acting as a flexible structure that divides space, controls light, and functions like furniture. It separates areas while maintaining openness, and can also serve as a canopy or support projection mapping like a media façade. The elastic fabric can be used as urban furniture—such as a sofa or hammock—and, as it moves with the wind, creates tactile and visual variation while shaping the atmosphere. In this sense, the fabric wall is not a fixed architectural element, but a dynamic, sensory medium that transforms space and user experience.




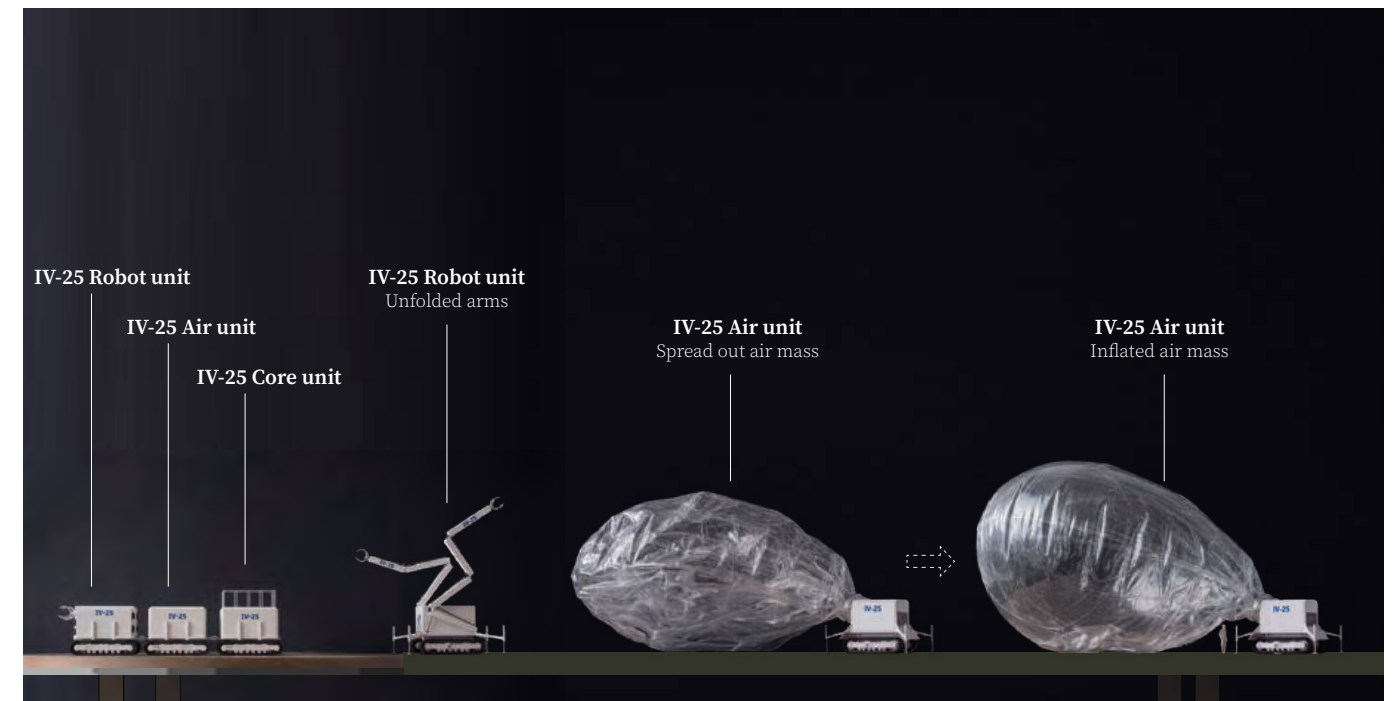


Photo. 1:50 model





At present, Gwanghwamun Square—the only major civic plaza of its kind in Seoul—is characterized by an elongated rectangular form. This configuration, aligned with the linear axis of Sejong-daero, reinforces a unidirectional visual and spatial experience. As a result, the space appears to function less as a site for listening and dialogue across differences, and more as a platform for one-way “expression.”

CITY SEQUENCE.

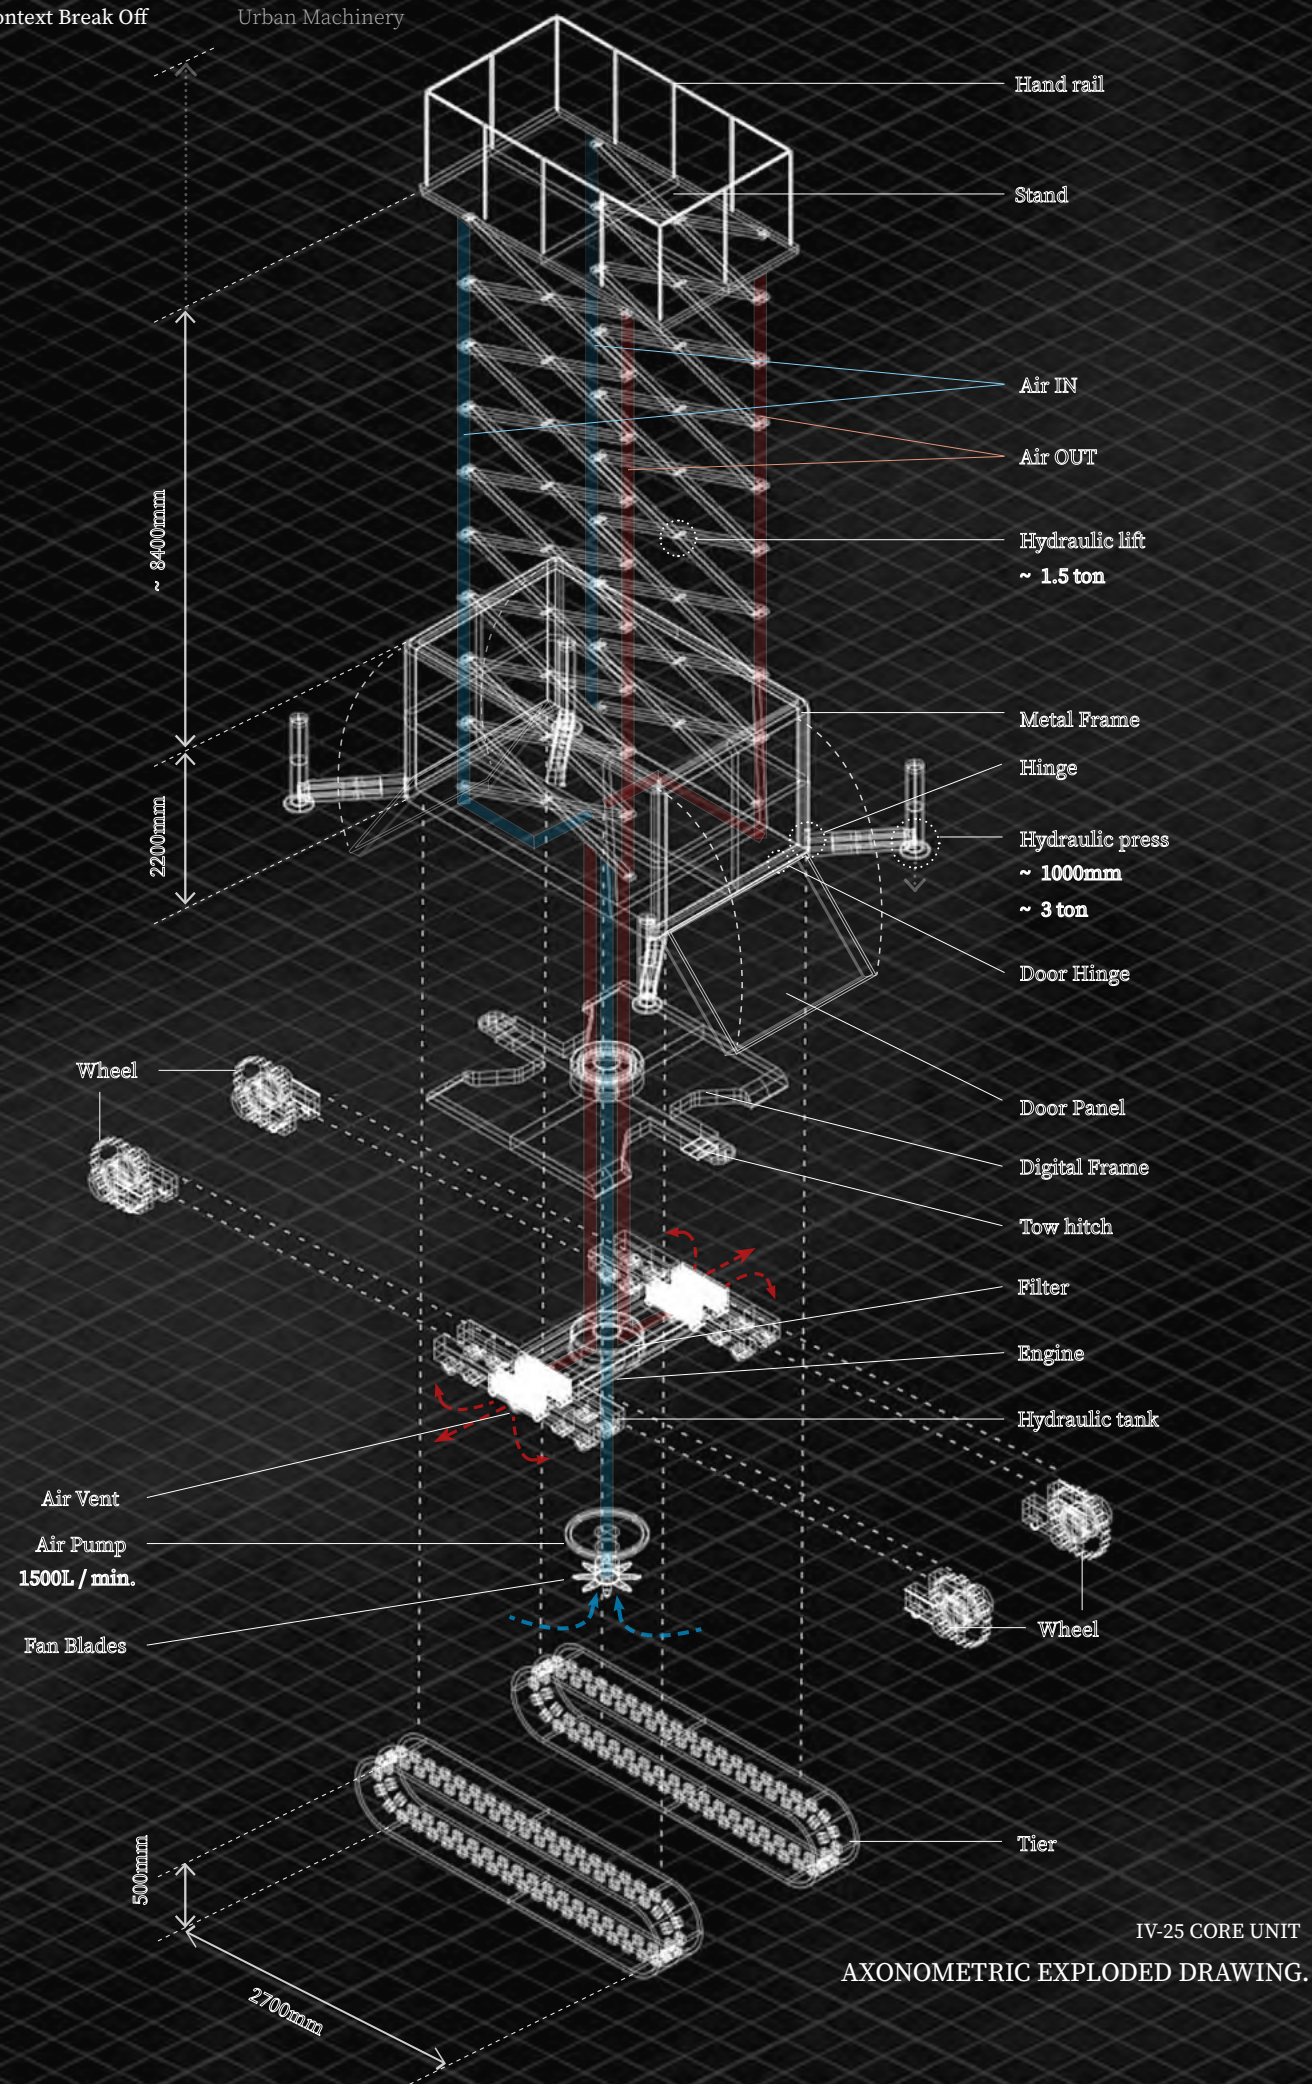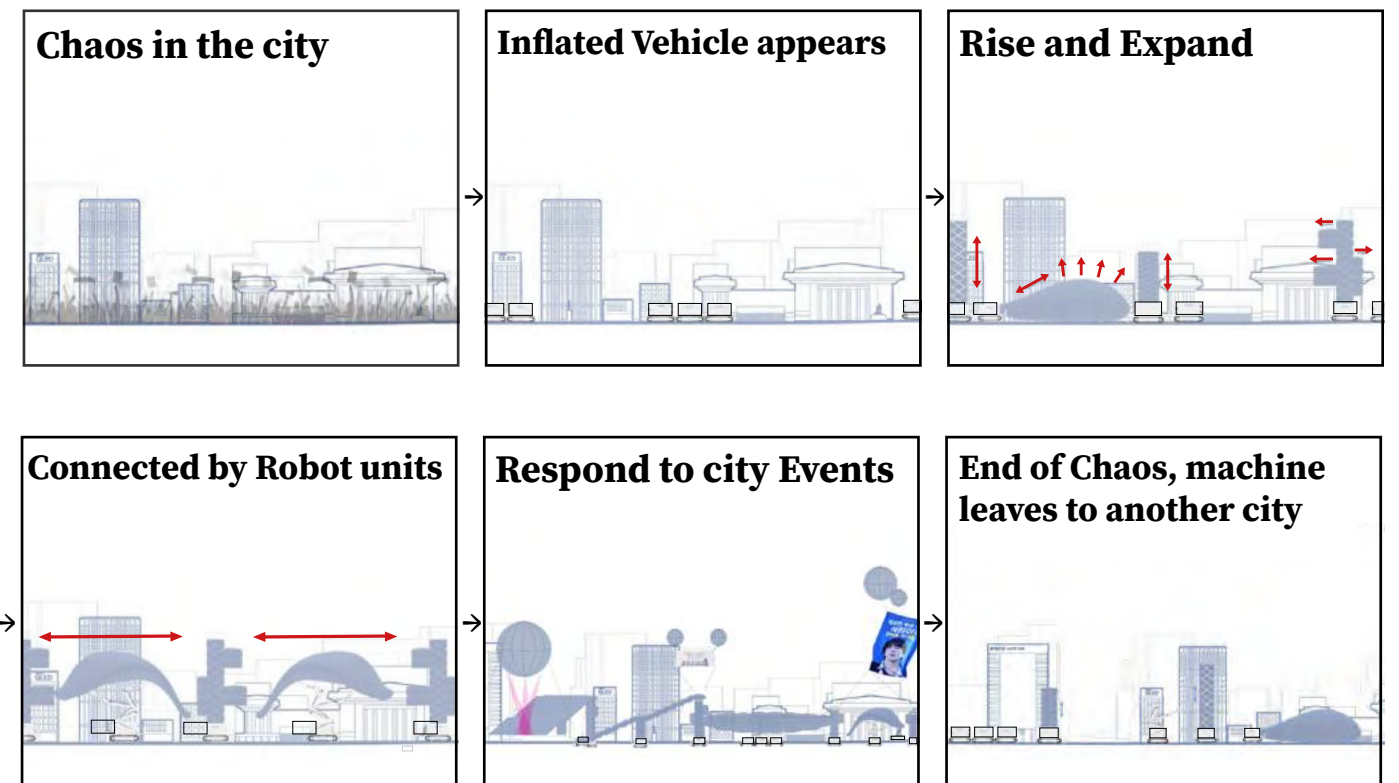


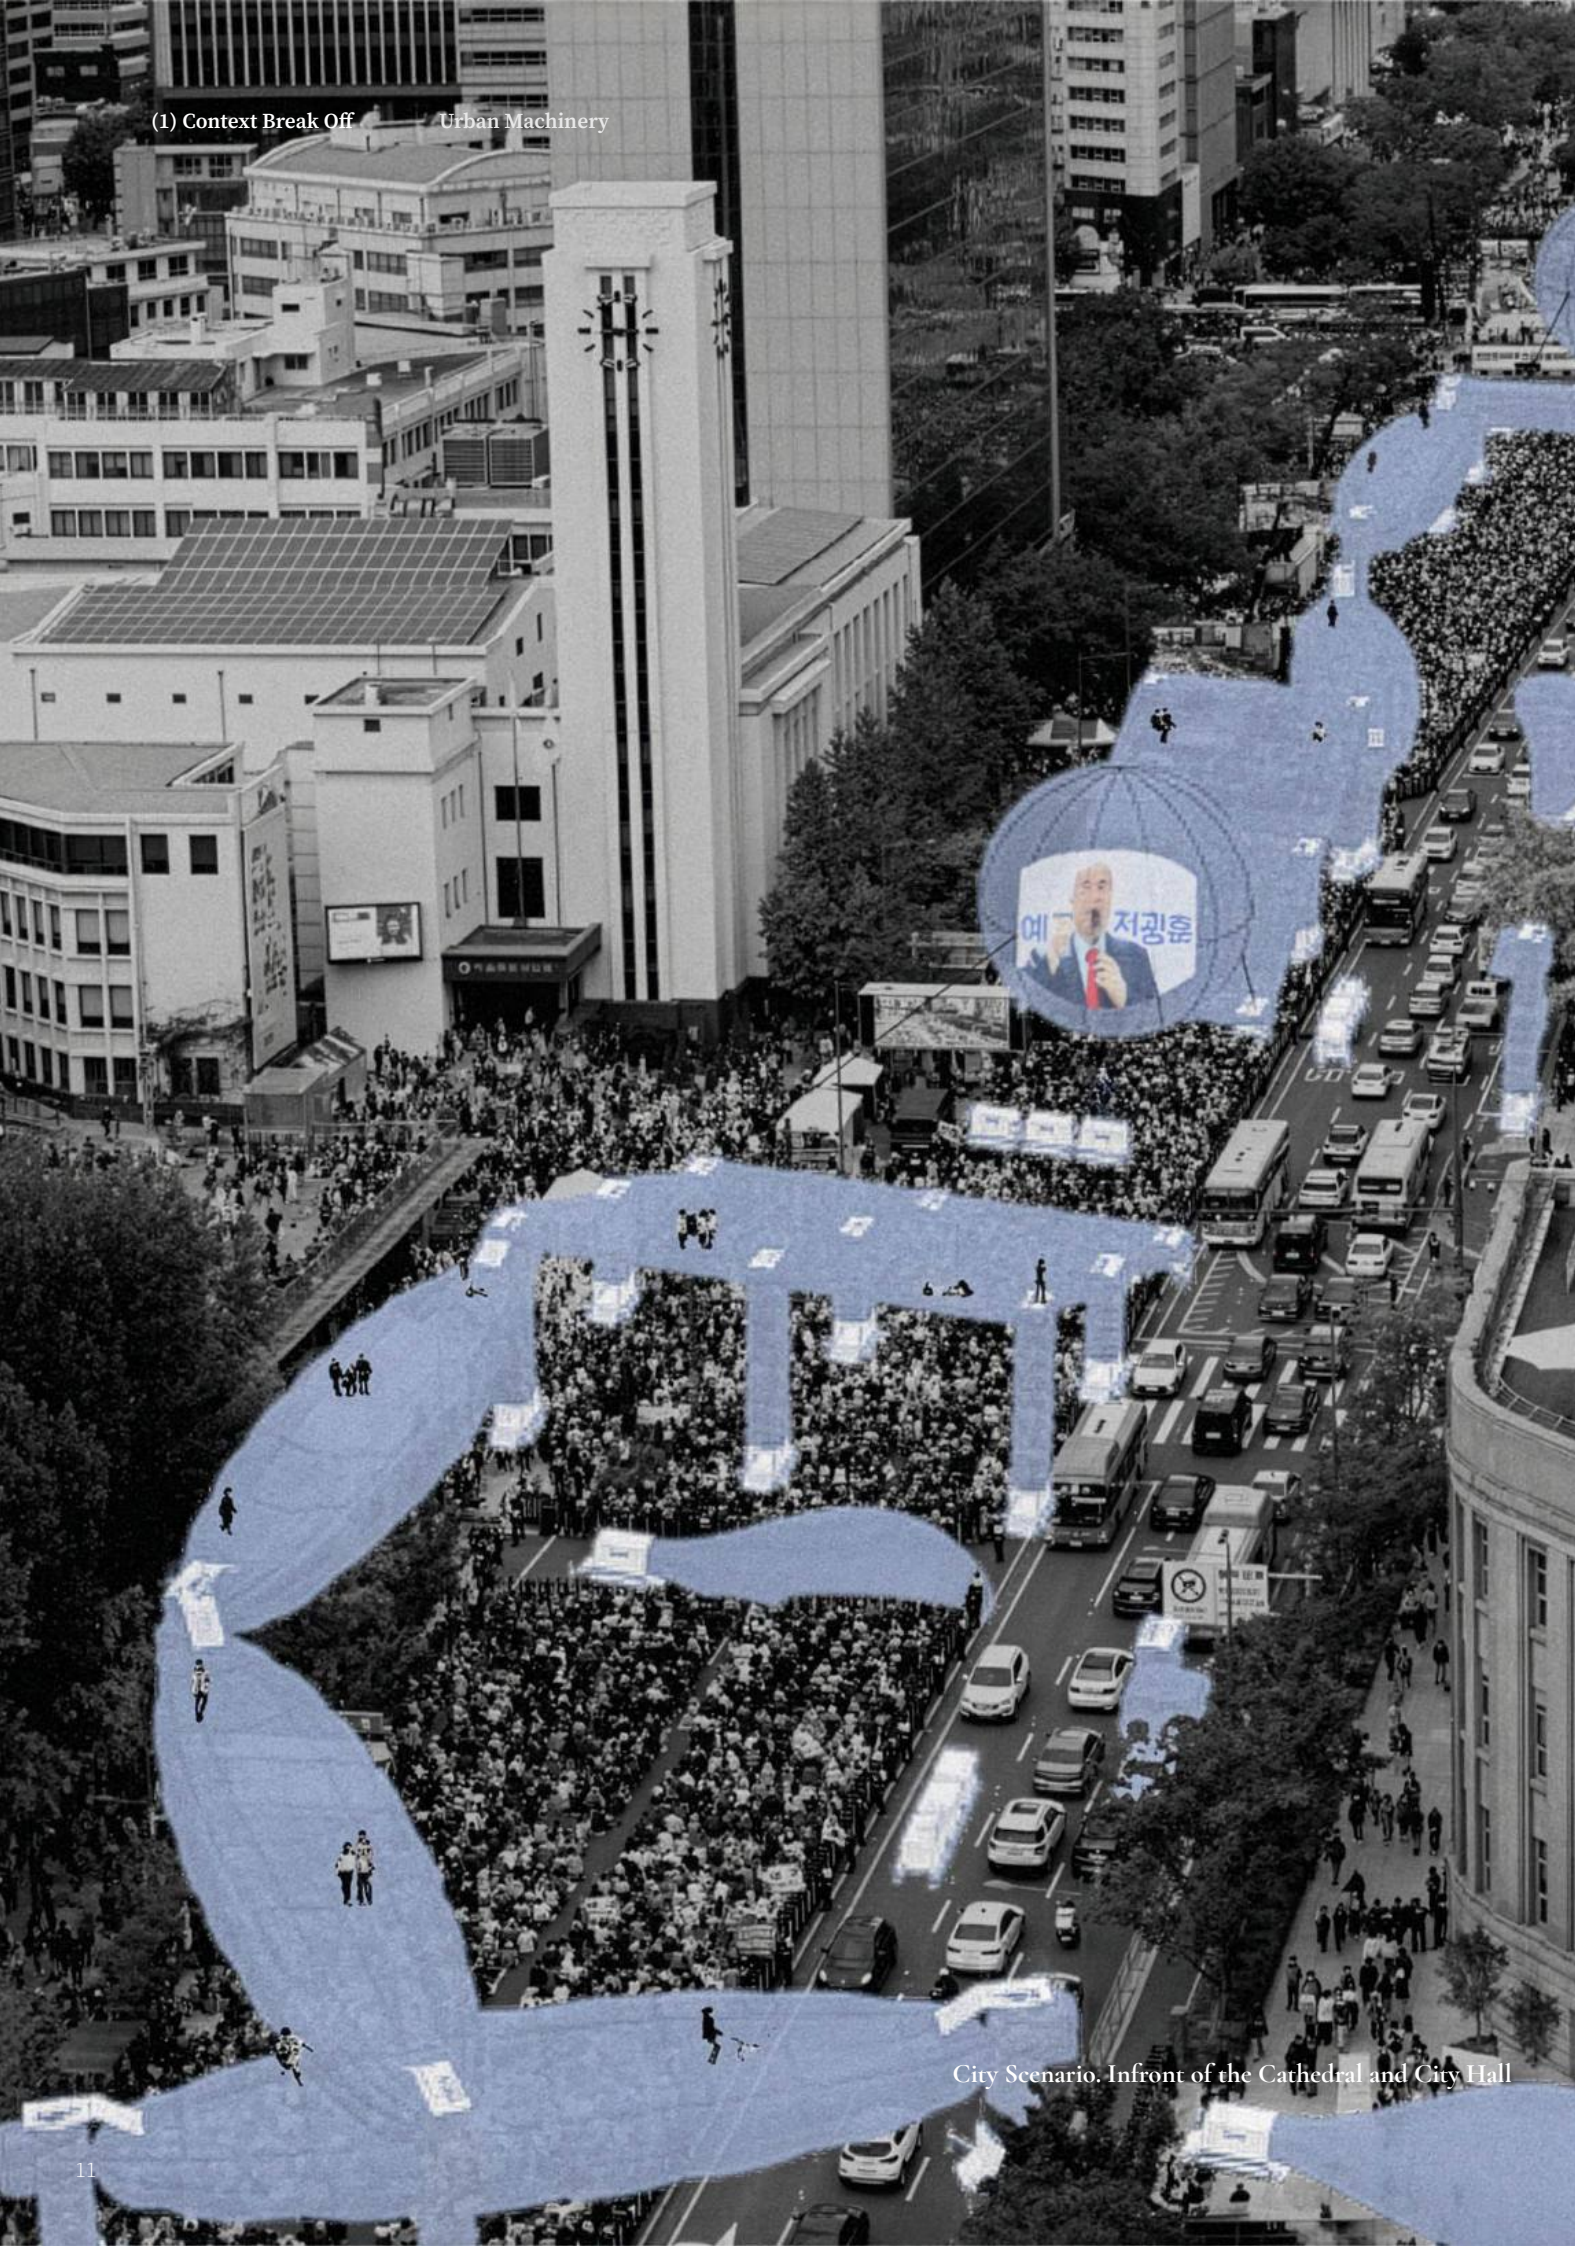


City Scenario. Infront of the Cathedral and City Hall

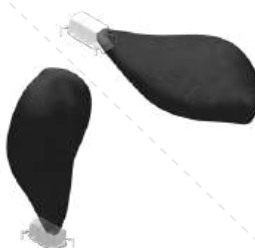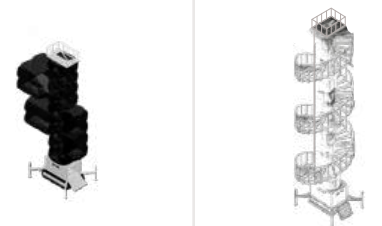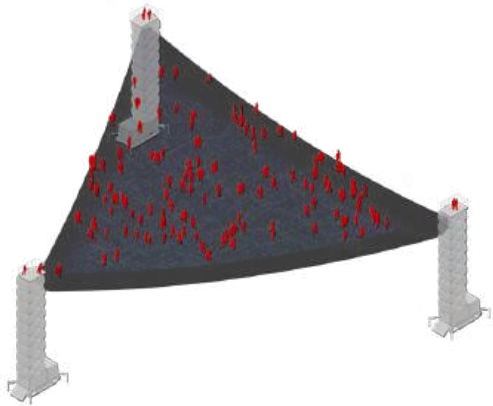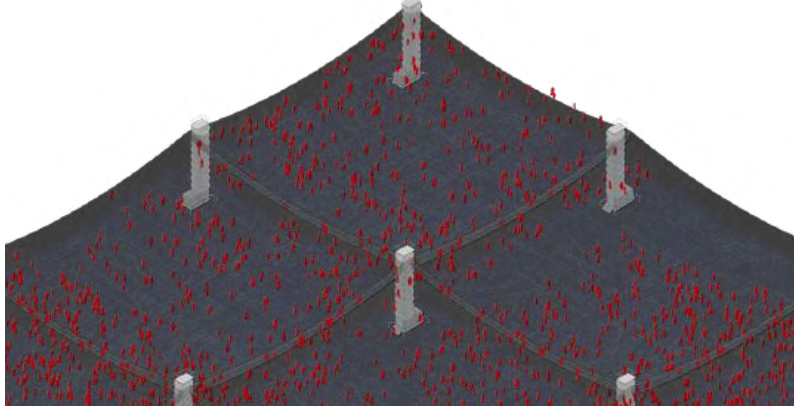 AXONOMETRIC 01. IV-25 Conclusion	 AXONOMETRIC 02. IV-25 air unit	 AXONOMETRIC 03. IV-25 core unit	 AXONOMETRIC 04. IV-25 robot unit	 AXONOMETRIC 05. IV-25 robot unit Unfolded arms
 AXONOMETRIC 06. IV-25 air unit Screen mode_OFF	 AXONOMETRIC 07. IV-25 air unit Screen mode_ON	 AXONOMETRIC 08. IV-25 air unit Stretched vertical / horizontal	 AXONOMETRIC 09. IV-25 air unit Air dome mode	 AXONOMETRIC 10. IV-25 robot unit Hanging the air mass
 AXONOMETRIC 11. IV-25 air unit Dome screen mode_OFF	 AXONOMETRIC 12. IV-25 air unit Dome screen mode_ON	 AXONOMETRIC 13. IV-25 core unit Expanded mode	 AXONOMETRIC 14. IV-25 core unit Circular core mode	
 AXONOMETRIC 15. Bridge mode 2 core unit + 1 air unit	Seats provide people to watch something together, which could make the common experience to each other. No matter what side you are, no matter what religion you are, no matter what gender you are, we just need to talk each different person.  AXONOMETRIC 16. Air Seat mode 6 core unit + 2 air unit	 AXONOMETRIC 17. Long Bridge mode N core unit + (N-1) air unit	 AXONOMETRIC 17. Forum mode 24 core unit + 9 air unit	
 AXONOMETRIC 18. Plaza mode_ about 30 people to accomodate	 AXONOMETRIC 19. Square mode_ about 50N people(*N core unit + 1/4 air unit)			

City Scenario 02. View infront of the Cathadral, preparing the mass

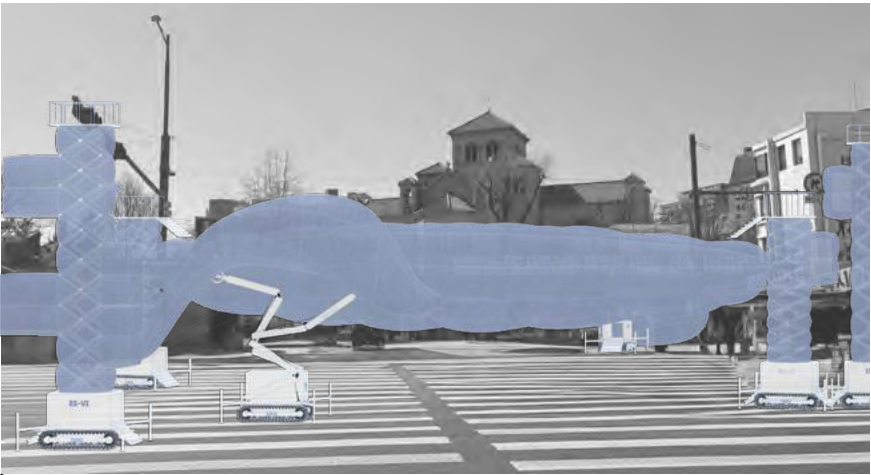


City Scenario 04. View under the IV-25 bridge

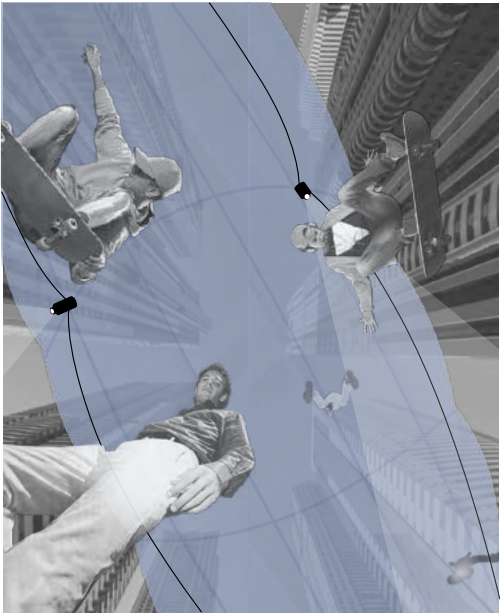

City Scenario 06. View infront of the Lee Soun-Shin Statue



City Scenario 08.
View infront of the Gyeongbokgung-Palace

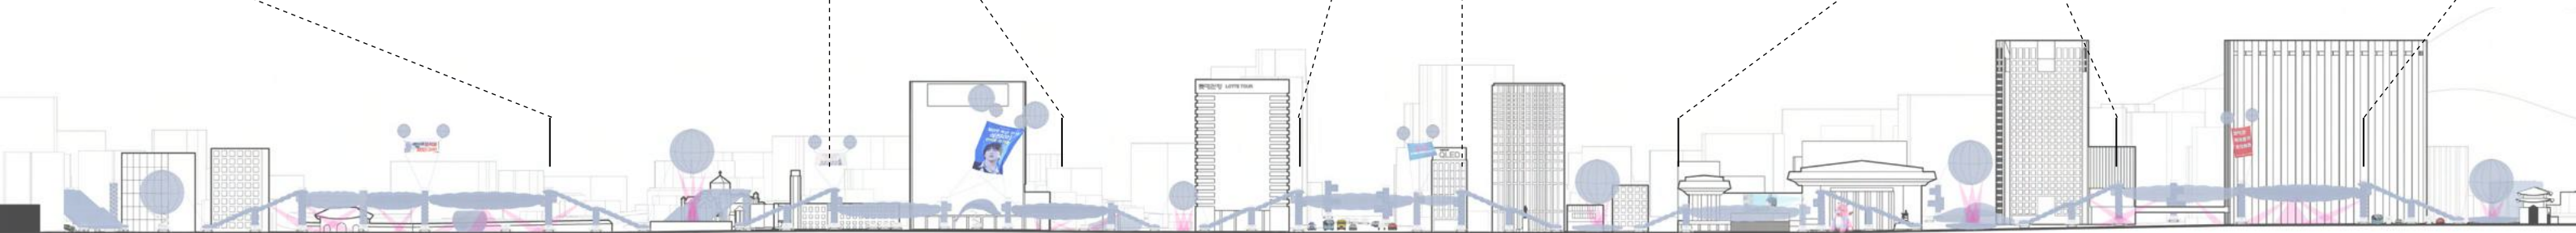

Duksugung Palace and City Hall
Demonstrate

Cathadral
Outdoor Mass

Hotel
Demonstrate

Lotte Mall
BTS Concert

Sejeong Road
Brdige

Lee Shunshin Statue
Debate

Culture Square & King Sejong Statue
Movie theater / Food Truck


Government Building
Demonstrate

Gyeongbuk Palace
Debate

City Scenario 01. View infront of the Duksugung Palace




City Scenario 03. View infront of the Hotel

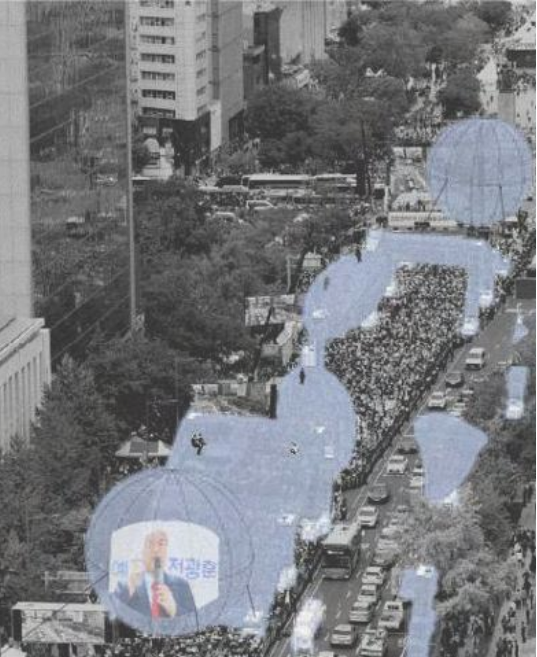

City Scenario 05.
View infront of the Jongmeo, the grave of the king




City Scenario 07.
View infront of the Sejong Culture Square

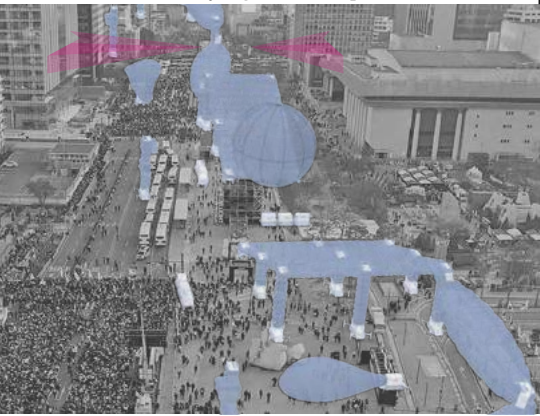

City Scenario 09.
Debating in front of Palace



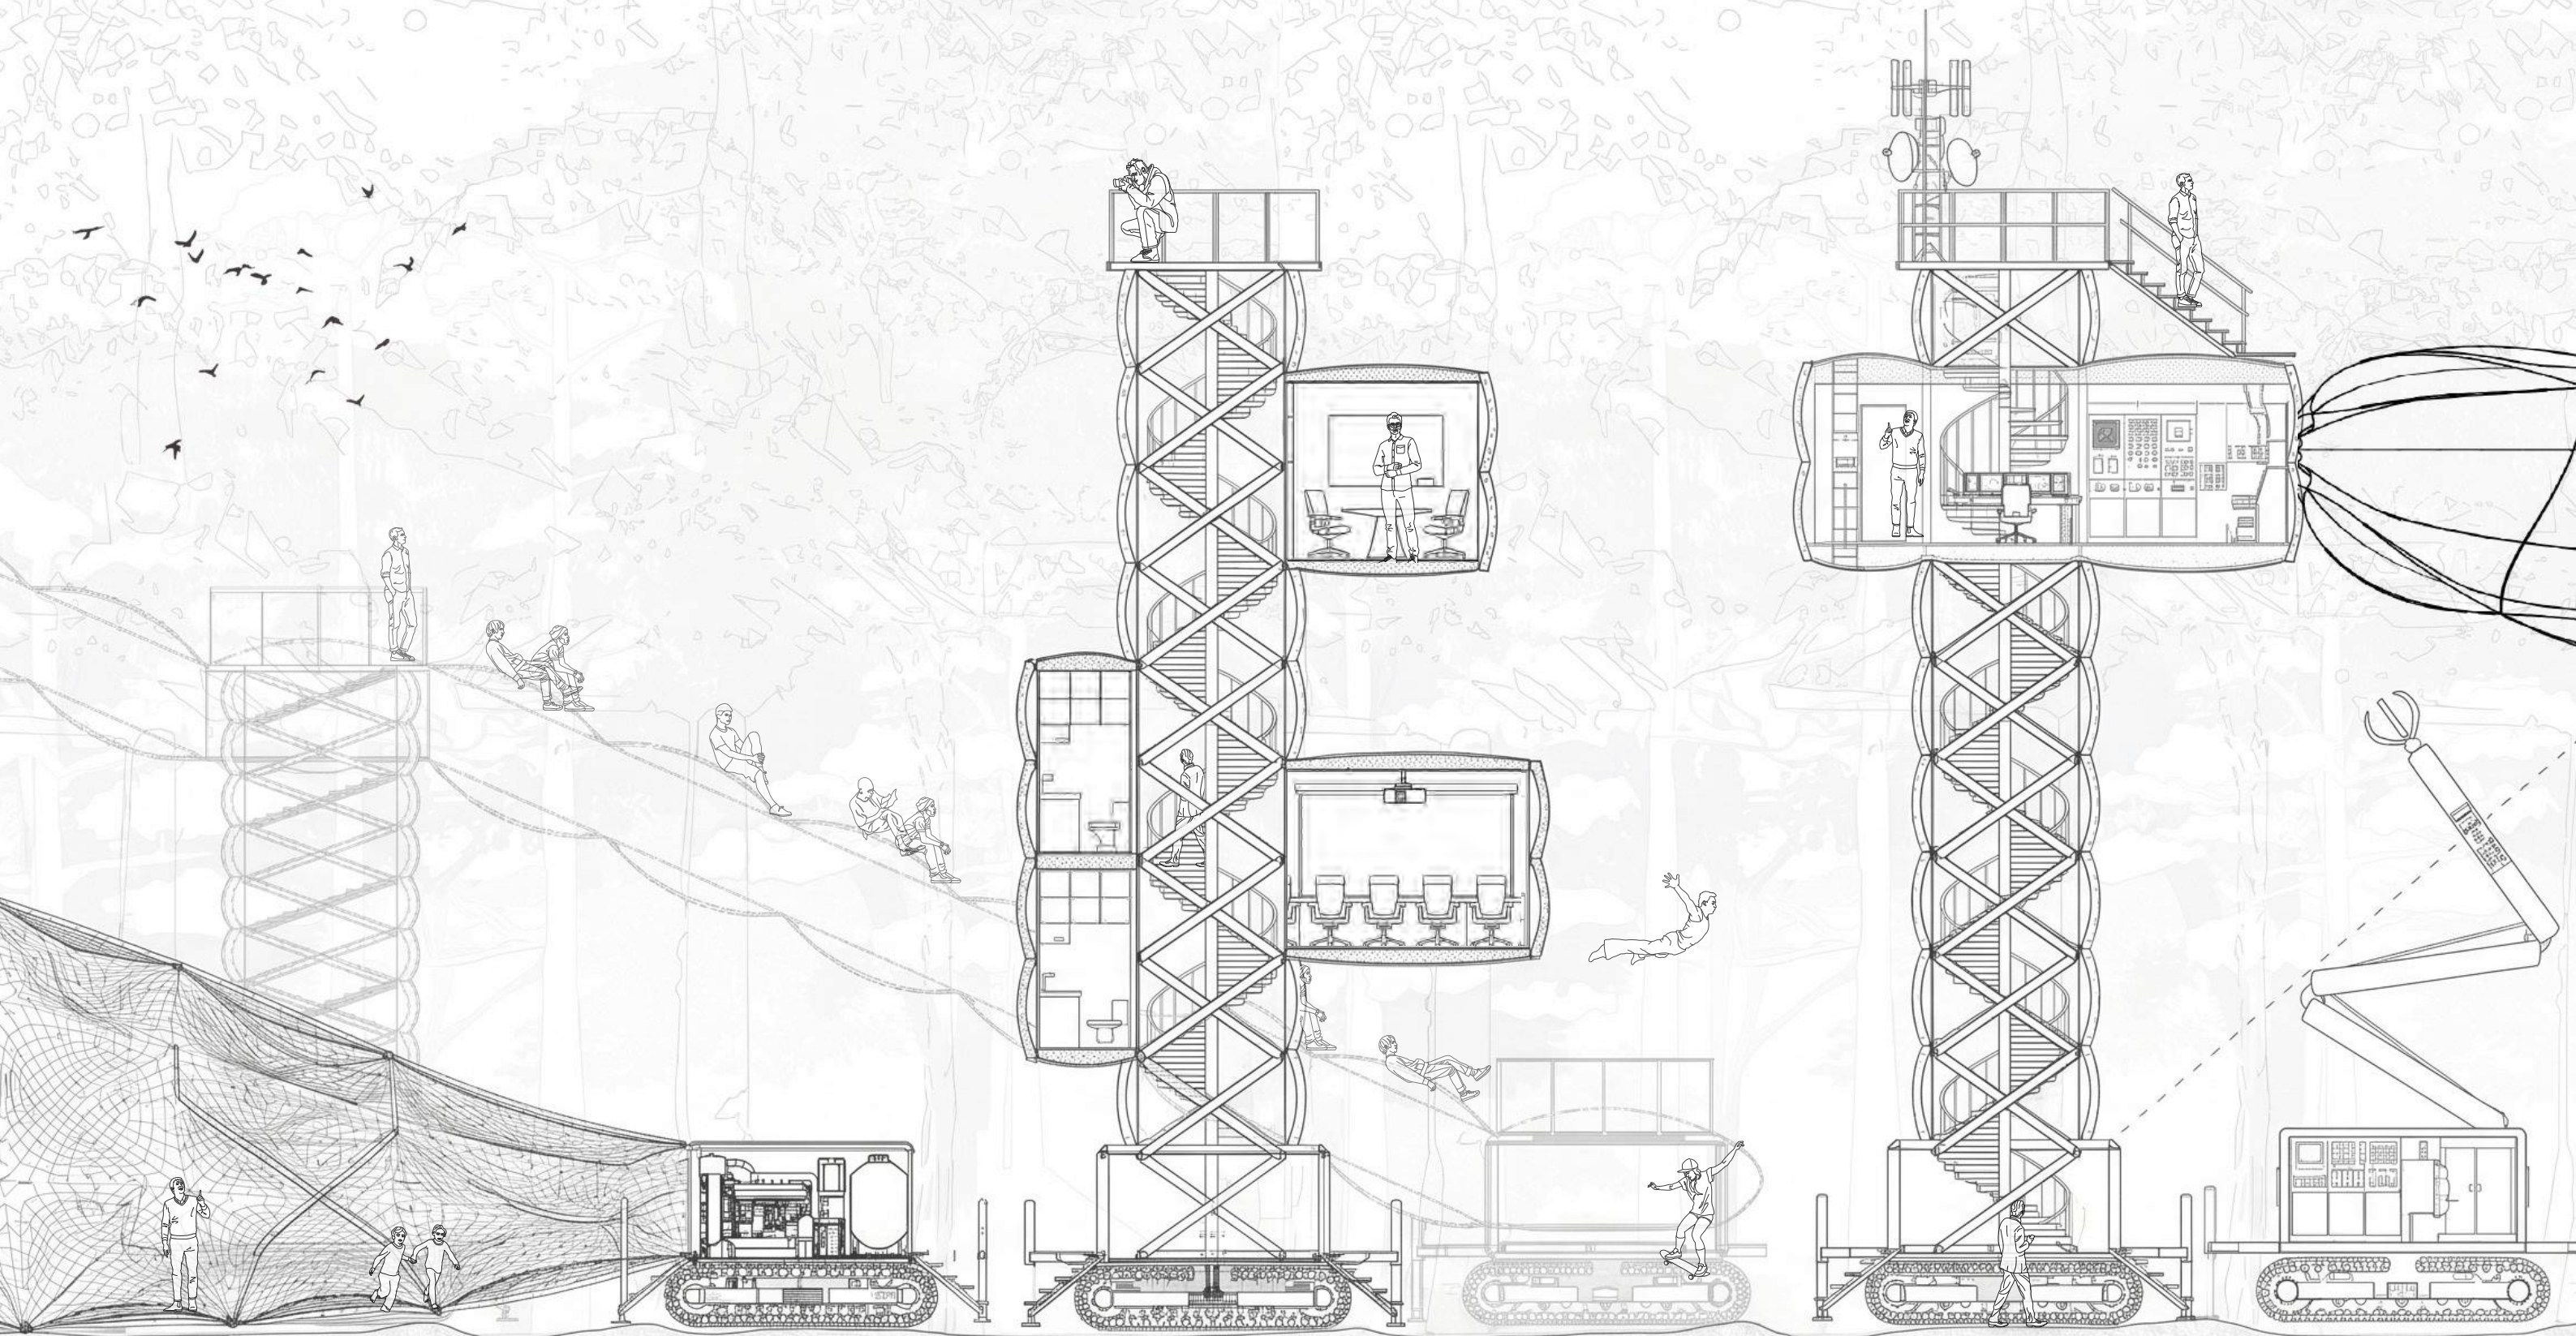

Inflated Vehicle : 'IV-25'

A wall made of large air-filled membranes goes beyond a simple boundary, acting as a flexible structure that divides space, controls light, and functions like furniture. It separates areas while maintaining openness, and can also serve as a canopy or support projection mapping like a media façade. The elastic fabric can be used as urban furniture—such as a sofa or hammock—and, as it moves with the wind, creates tactile and visual variation while shaping the atmosphere. In this sense, the fabric wall is not a fixed architectural element, but a dynamic, sensory medium that transforms space and user experience.



View 01. 1F outdoor_ Student in the park

02

FLOATING
GROUND


들어올린 땅

Project Information.	
• Location	: Bukak-dong, Seoul
• Year	: 2024 - 01
• Status	: Academic Study <i>(Individual)</i>
• Type	: Middle School
• Instructor	: Lee Seung-Tek

Prologue.


School is envisioned not just as an educational facility, but as an open and lively environment where students and children can freely run, play, and explore—blurring the boundary between learning and everyday life. Generous open spaces and interconnected pathways encourage spontaneous movement, interaction, and play, allowing the school to function as a shared landscape that supports both education and the everyday rhythms of the neighborhood. In the end, it becomes less a school you simply attend, and more a place you naturally drift through and stay.

SECTION A-A'

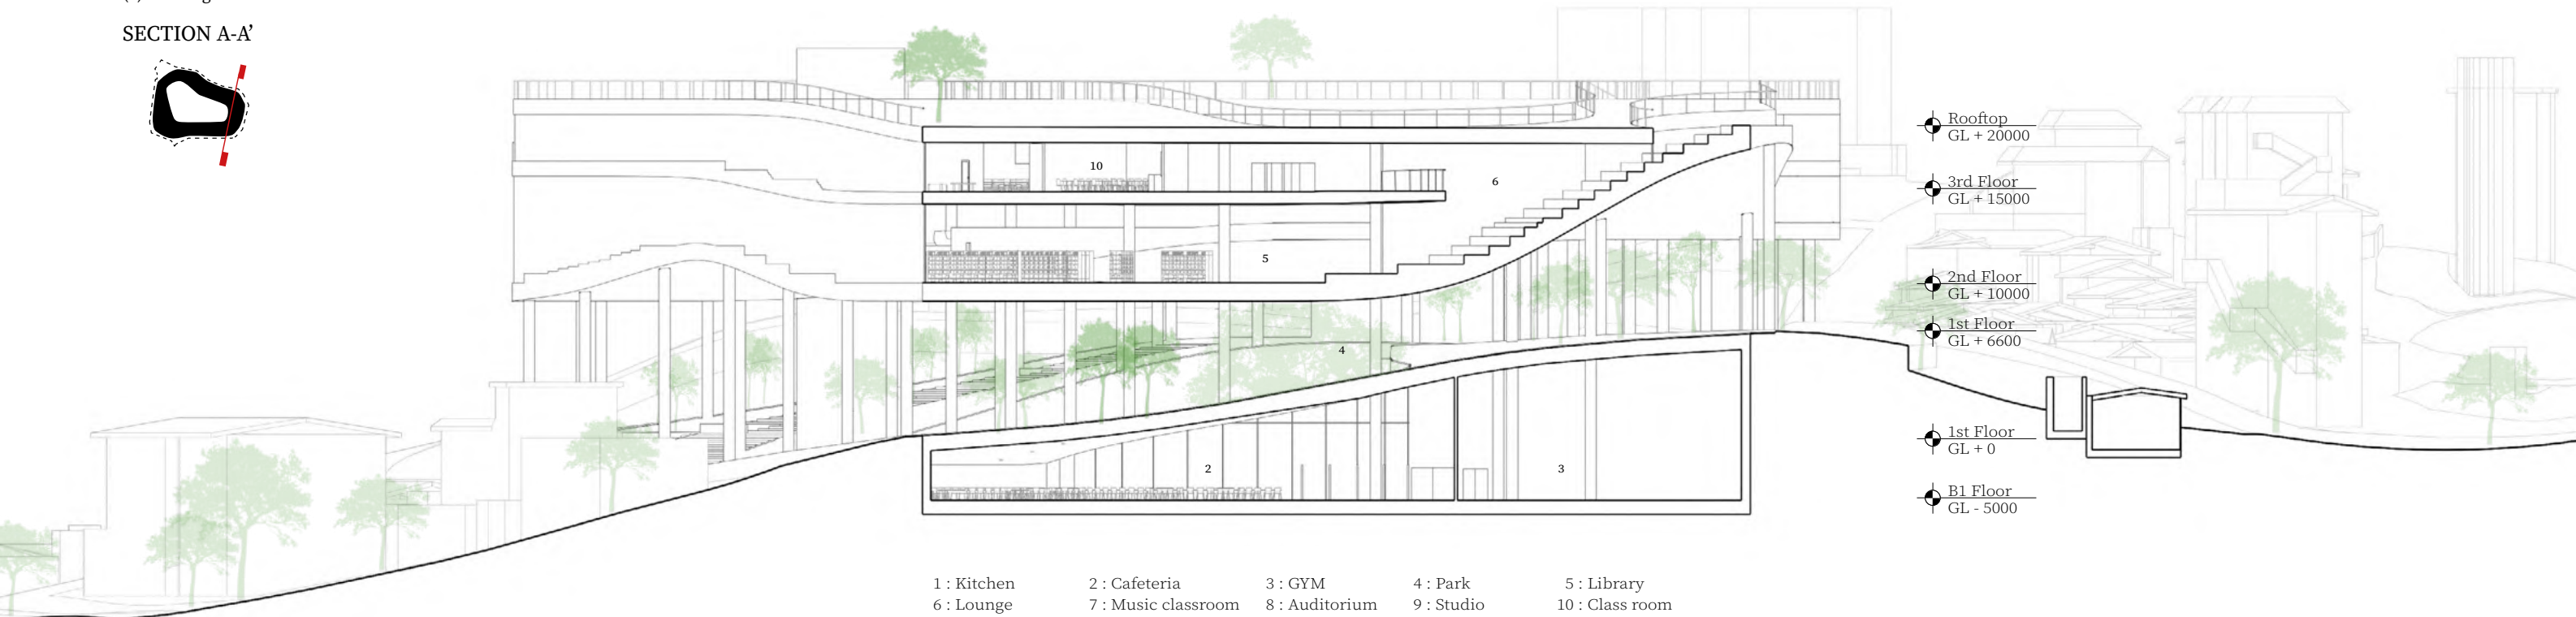


No Entry Trail_ Useless Green Area

Steep Slope

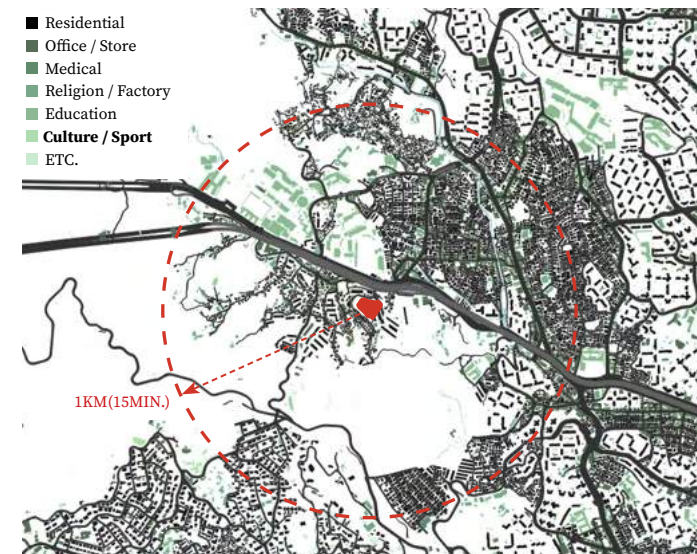


Lack of Community spaces and Cultural events

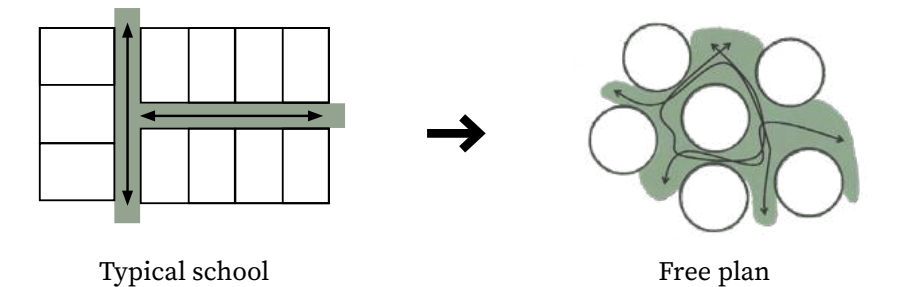

Typical school

Free plan

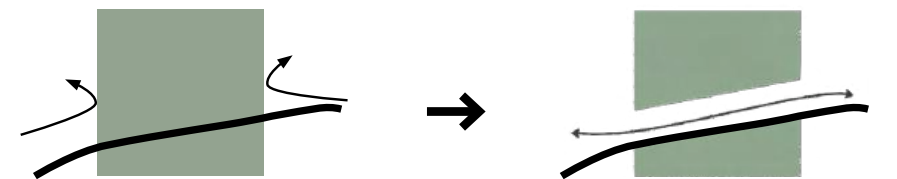


Typical slope


Both for students and local

This project proposes to introduce an open green space for residents in this small hillside neighborhood, offering a place that is both accessible and welcoming. At the same time, it envisions a connected spatial system that accommodates flexible circulation for students and supports a range of programs—fostering interaction between the school and the local community while extending the everyday use of the site beyond a single event.

Conventional schools often feel rigid and enclosed—defined by fixed layouts, controlled circulation, strict schedules, and a sense of predictability that can resemble confinement. In contrast, this proposal embraces openness and fluidity, offering a more liberated environment where movement is intuitive, spaces are adaptable, and daily experiences are less prescribed.

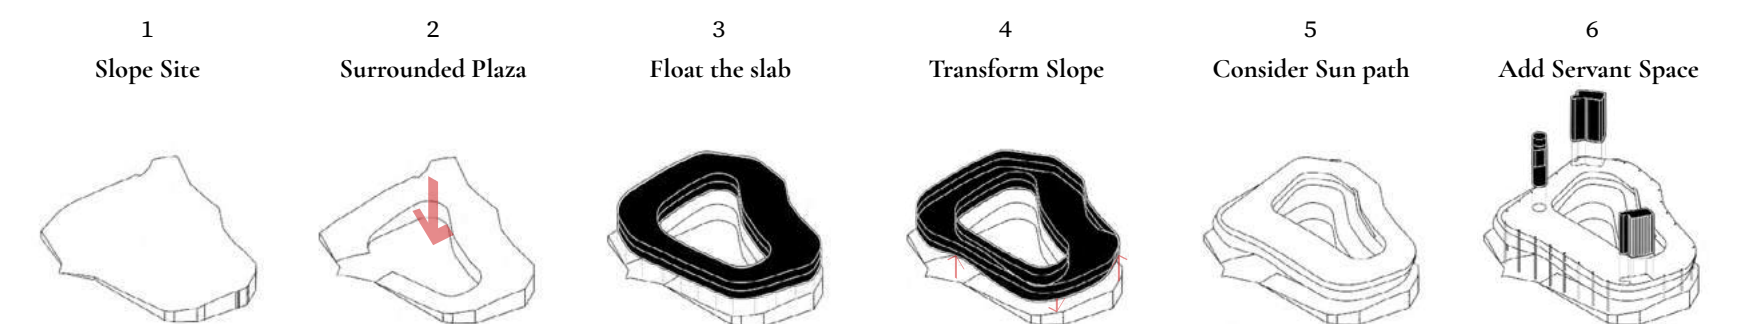

MASS PROGRESS. 1 - 2 - 3 - 4 - 5 - 6

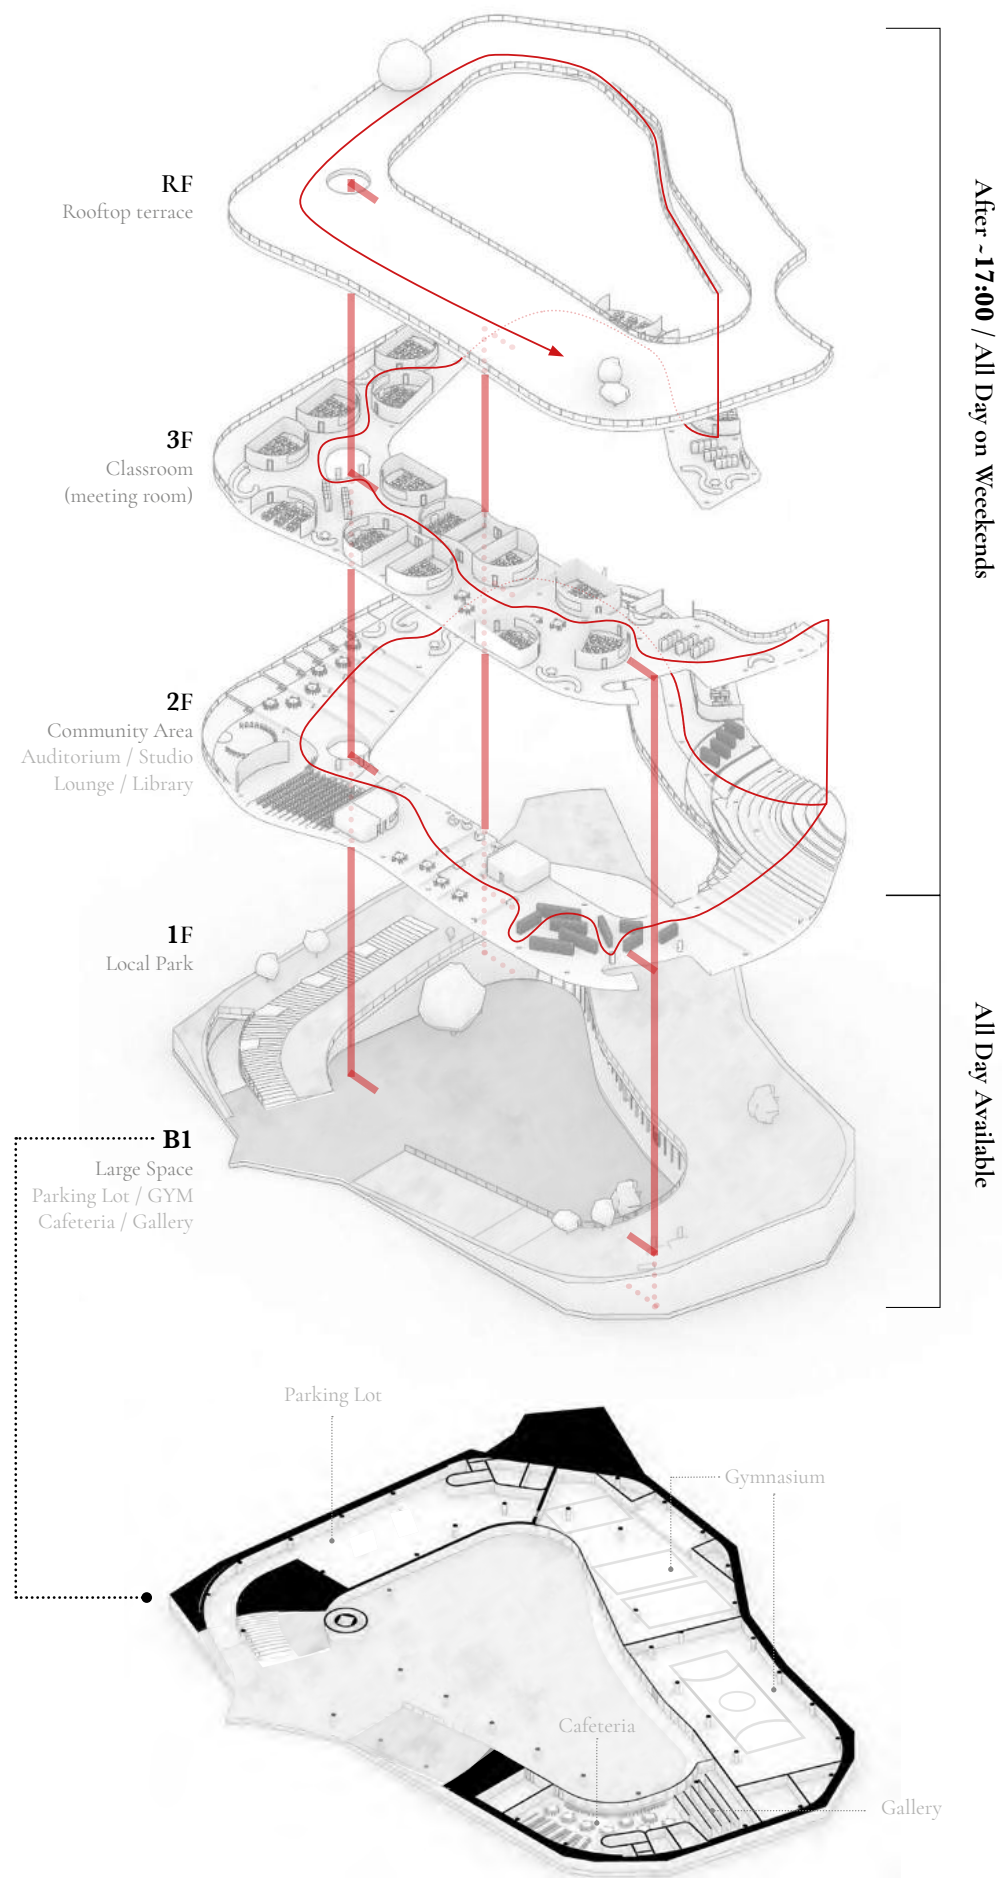


View 02. B1 outdoor_ Looking up

Although the area appears rich in greenery due to the surrounding mountains, there is a lack of accessible and livable open spaces where residents can comfortably gather and stay. Within this context, Bukak-dong hosts a local festival called “Bukakjae,” centered around Bukak Middle School located on the site. Through food, performances, student concerts, and various shared activities, residents come together to build a sense of community and collective connection.



View 03. 1F outdoor_ Local people resting in the park

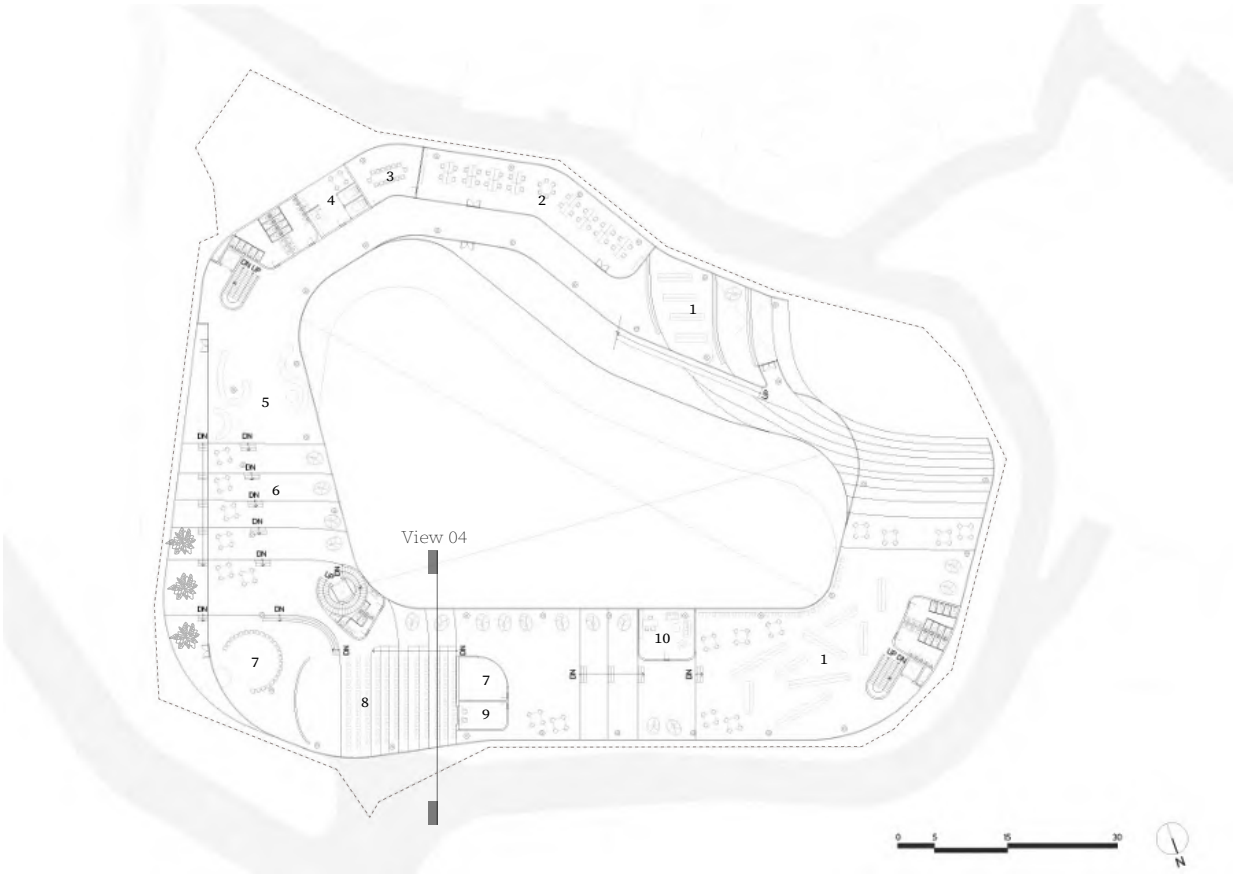

2nd Floor Plan 1 : Library 2 : Teacher's room 3 : Meeting room 4 : Nursing room 5 : Lounge
6 : Complex Hall 7 : Music classroom 8 : Auditorium 9 : Studio 10 : Counseling room



View 04. 2F Auditorium_ Students performing at the eve of the 'Bukak Local Festival'



3th Floor Plan 11 : Homebass 12 : Labatory 13 : Classroom 14 : Library



View 05. 3F Library_ Students reading books at the break time

(2) Floating Ground
SECTION B-B'

Middle School

2024-01



Rooftop
GL + 19000

3rd Floor
GL + 15000

2nd Floor
GL + 10000

1st Floor
GL + 5400

B1 Floor
GL - 5000

- 1 : Kitchen
6 : Lounge
2 : Cafeteria
7 : Music classroom
3 : GYM
8 : Auditorium
4 : Park
9 : Studio
5 : Library
10 : Class room

SECTION DETAIL B-B'

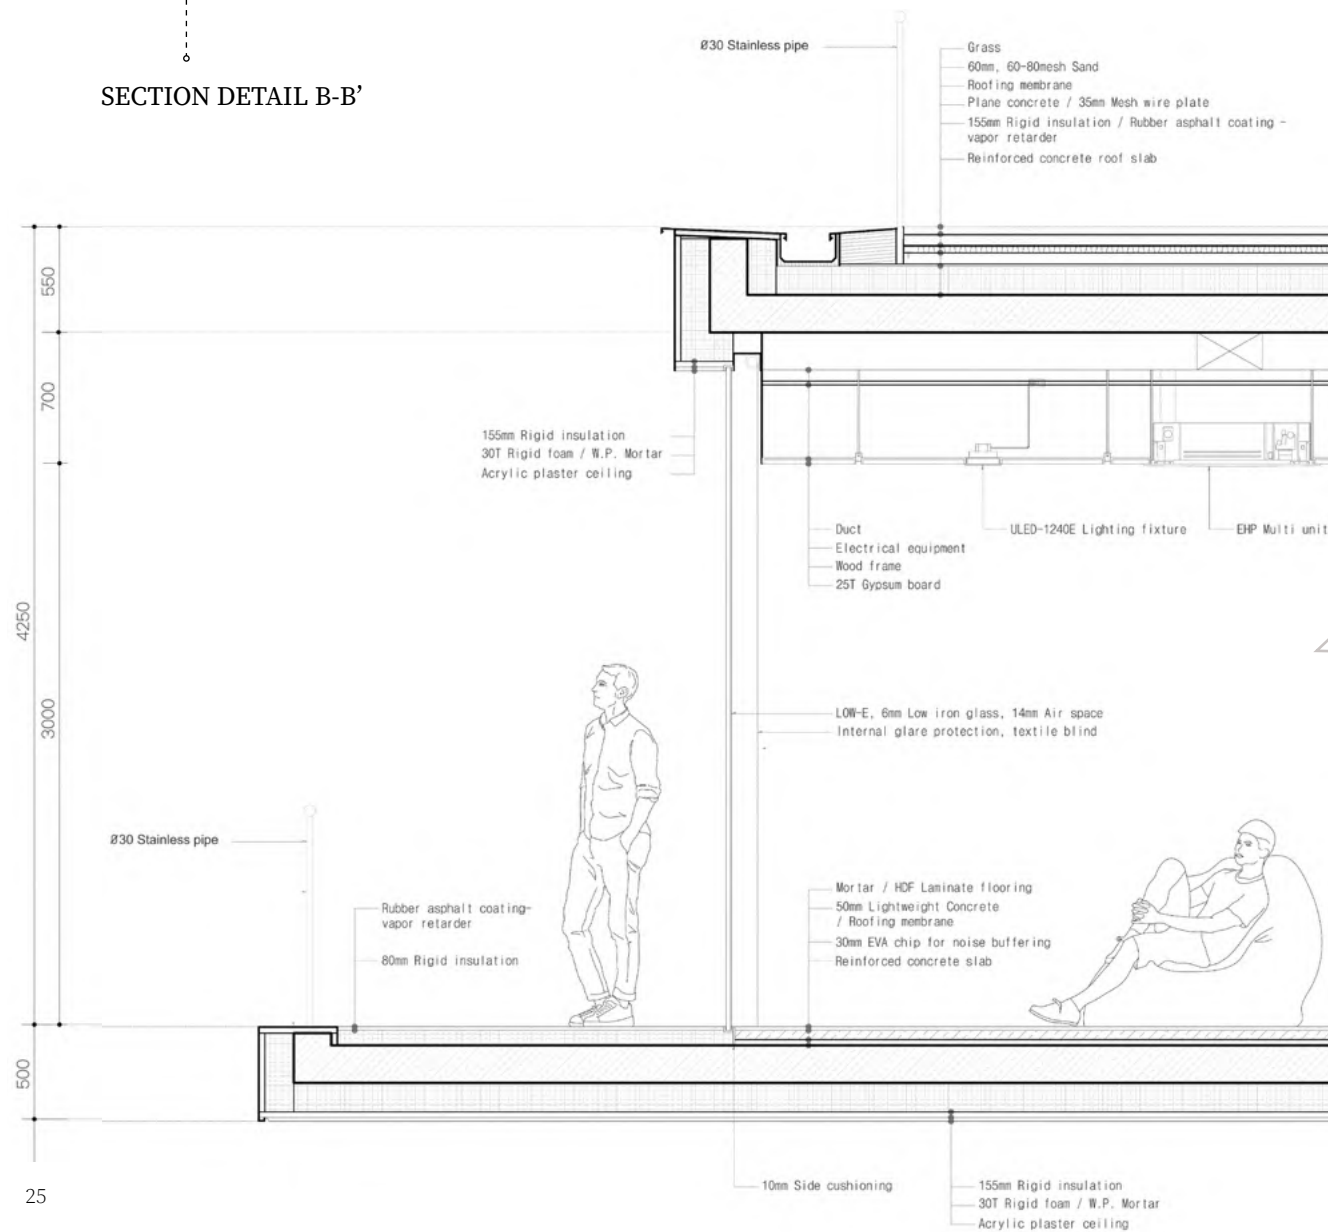



Photo. 1:200 model image_ North side facade



Photo. 1:200 model image_ South west side view




Photo. 1:200 model image_ Top view

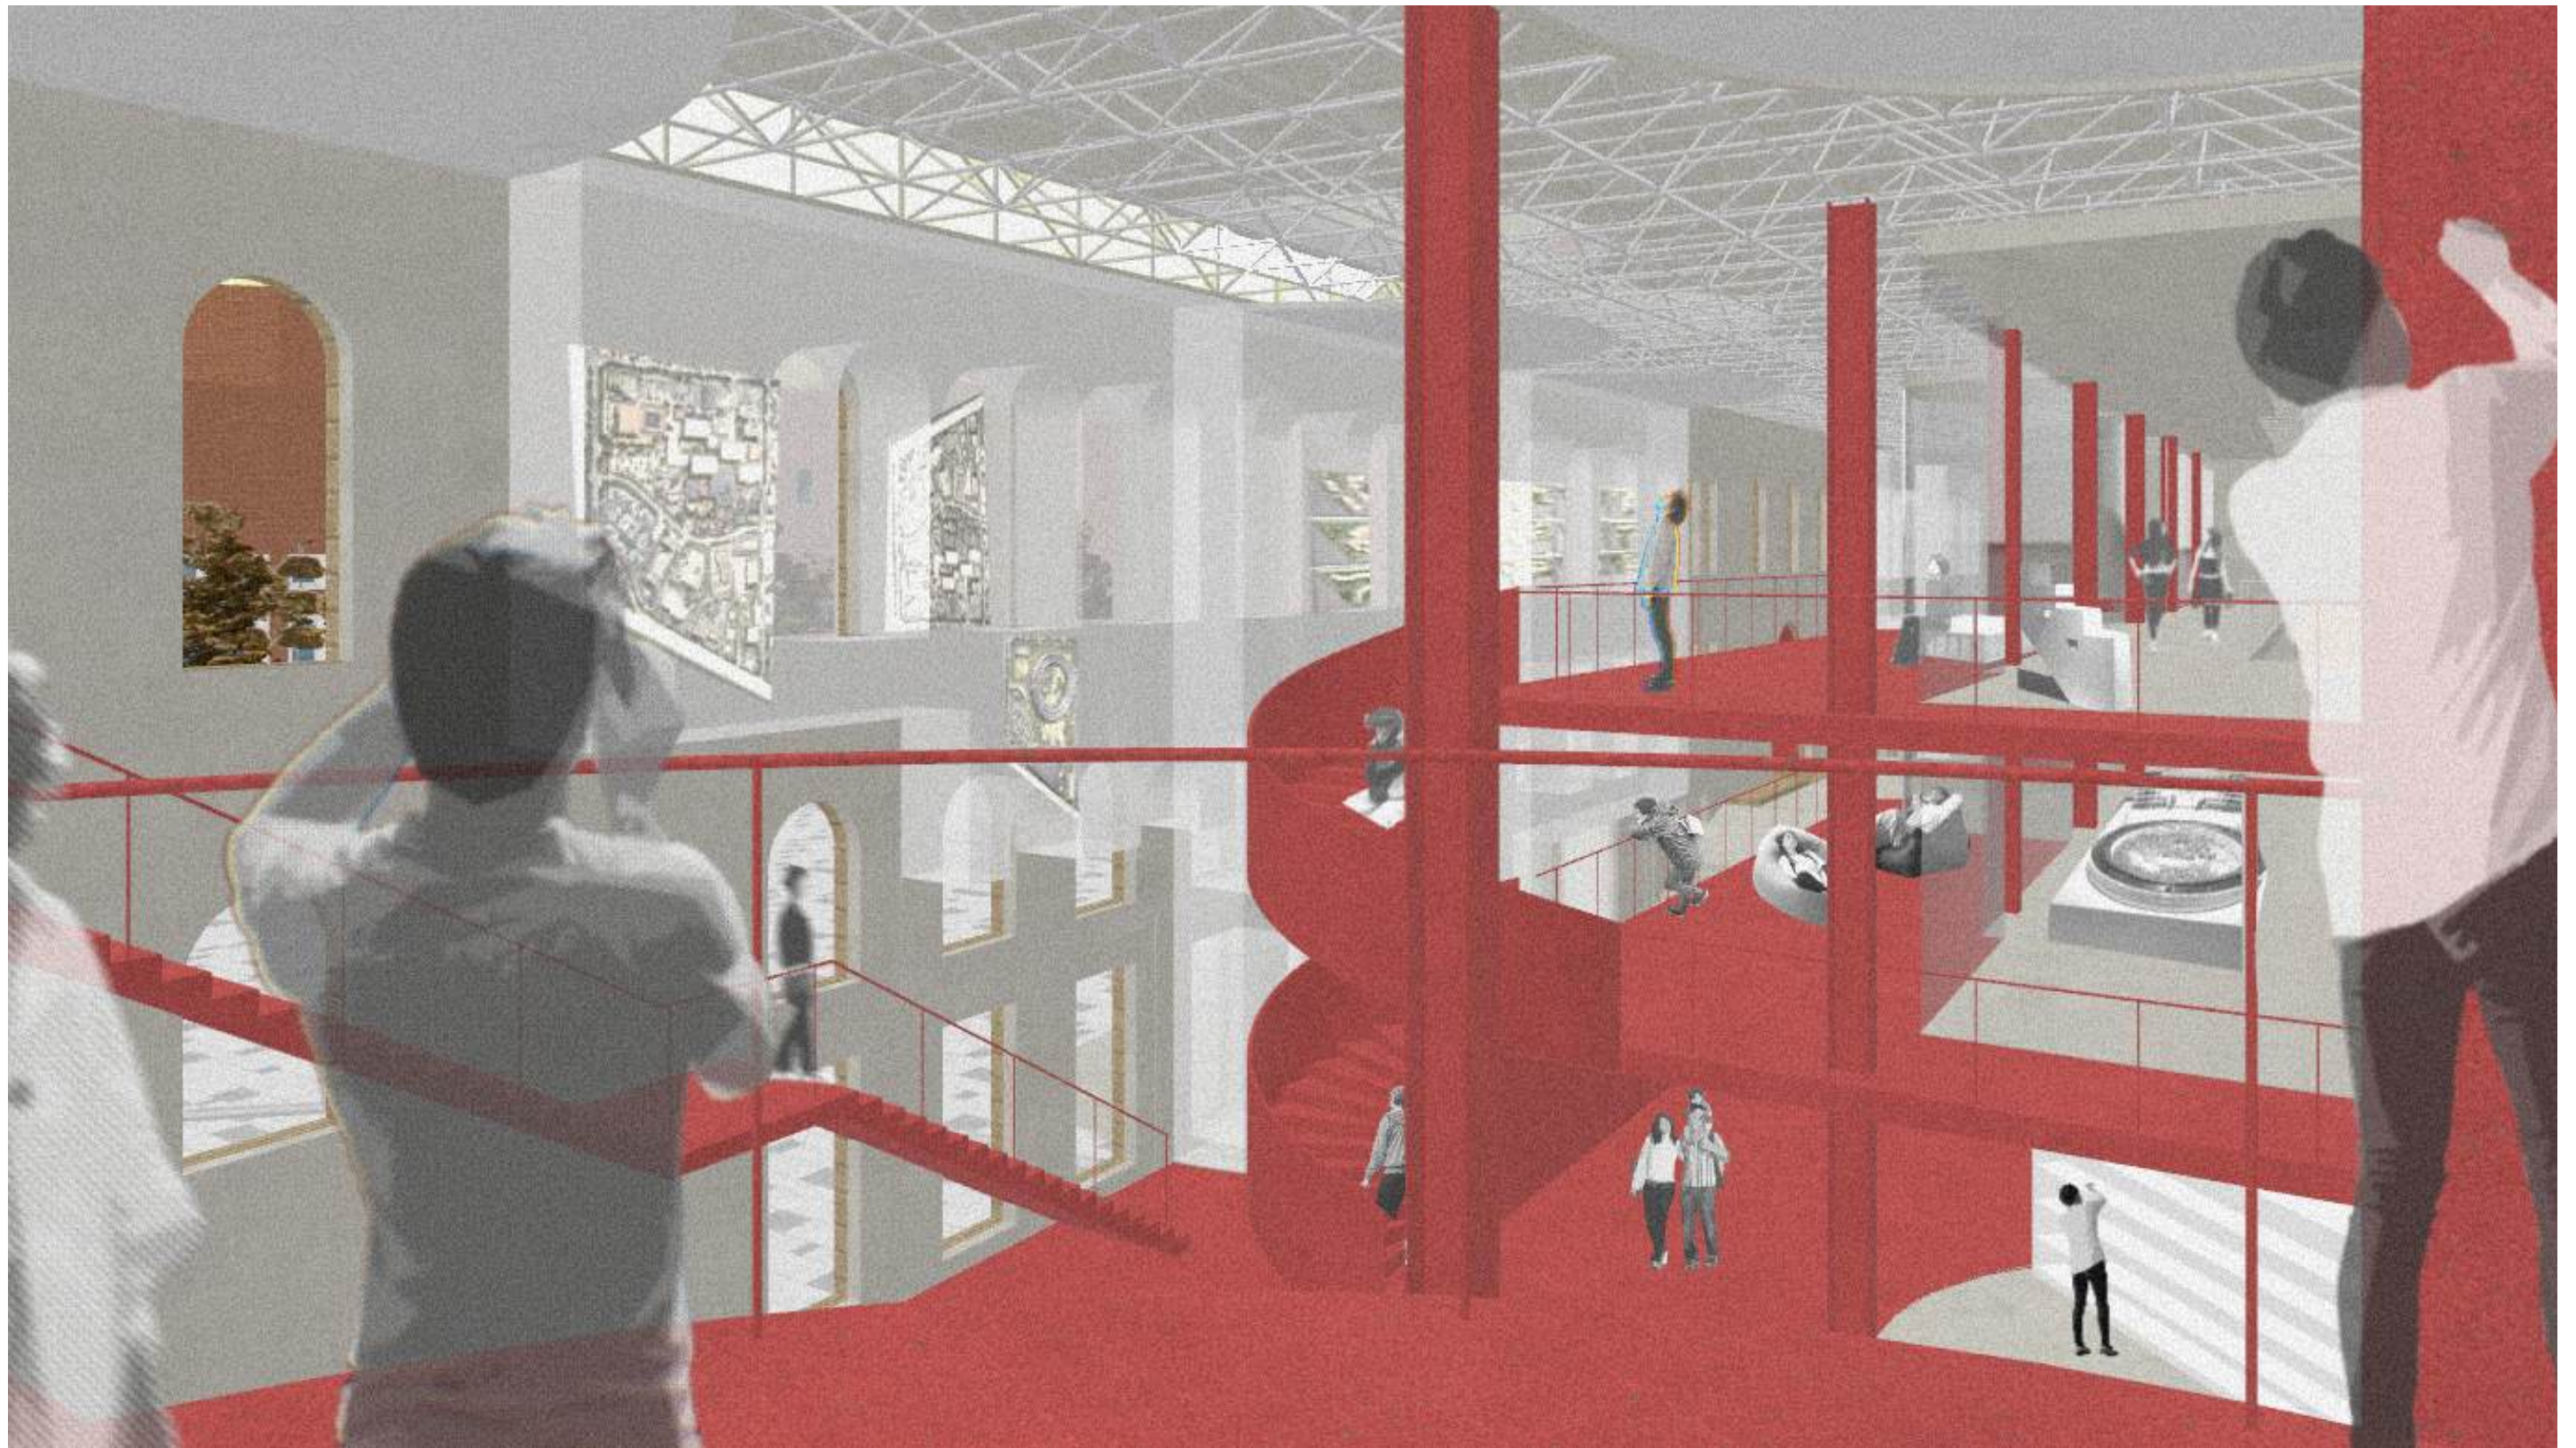

03 MUSEUM IS MOVING

박물관이 움직인다

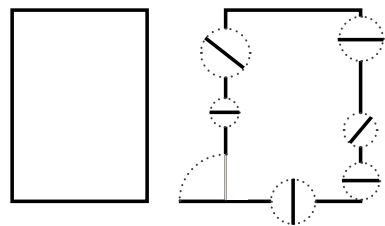


Project Information.


- Location : Haehwa-dong, Seoul
- Year : 2024 - 02
- Status : Academic Study (*Individual*)
- Type : Renovation Project
- Instructor : Seongbeom Mo

Prologue.


Due to the nature of 'Marronnier Park', a large gathering of people who are noated to architecture. It is difficult for the general public to understand intangible culture in the form of records such as drawings or texts. The architectural museum should not be limited to archives or model exhibitions, but should be a spatial experience in architecture itself. This site needs an architectural museum which could accomodate various programs and present various spaces accordigly. Hence, the project introduces a multi-sensory spatial network, reinterpreting traditional archives into a lived architectural experience.

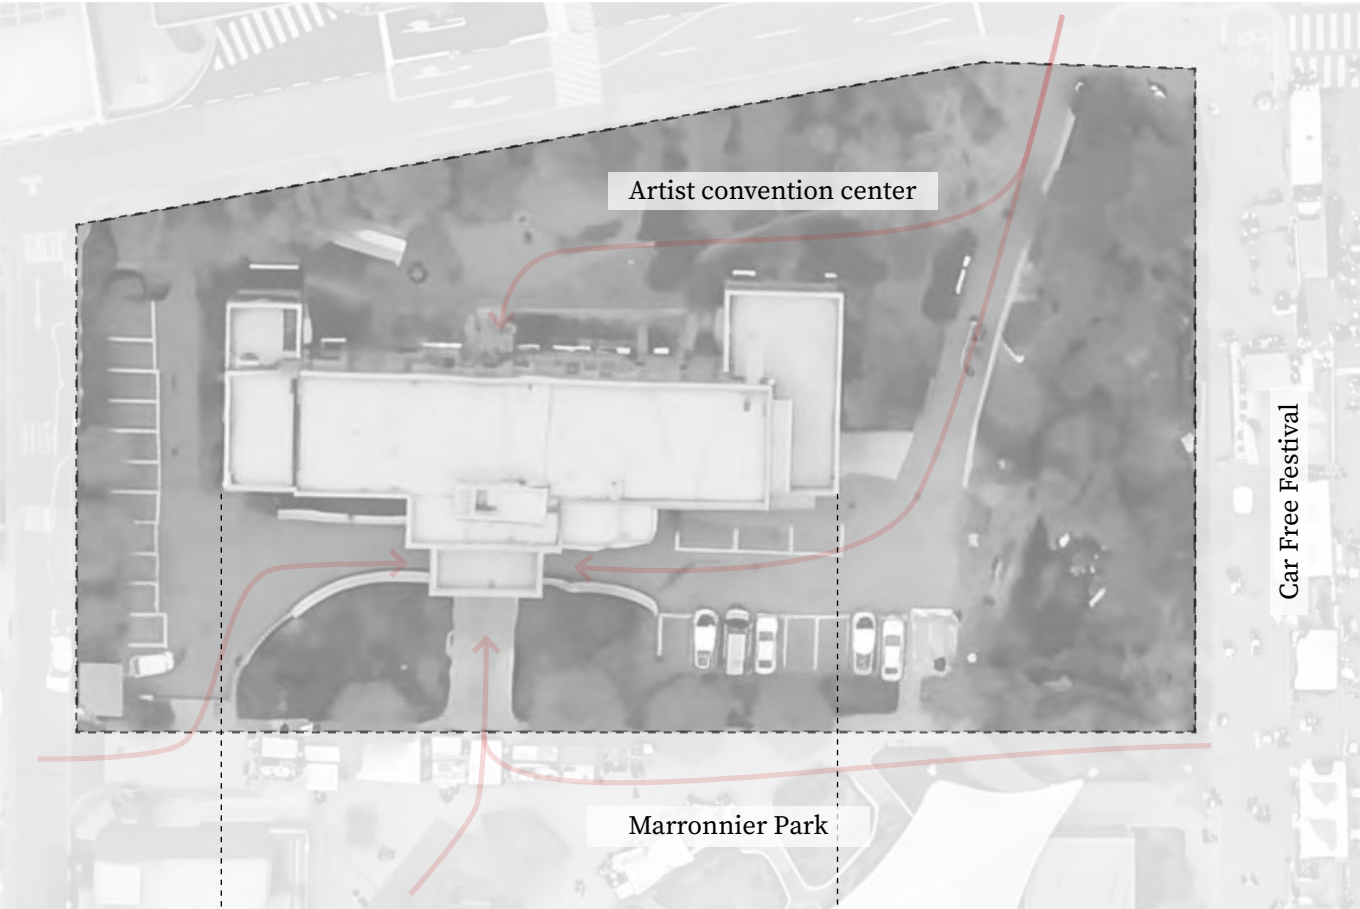

Old Facade

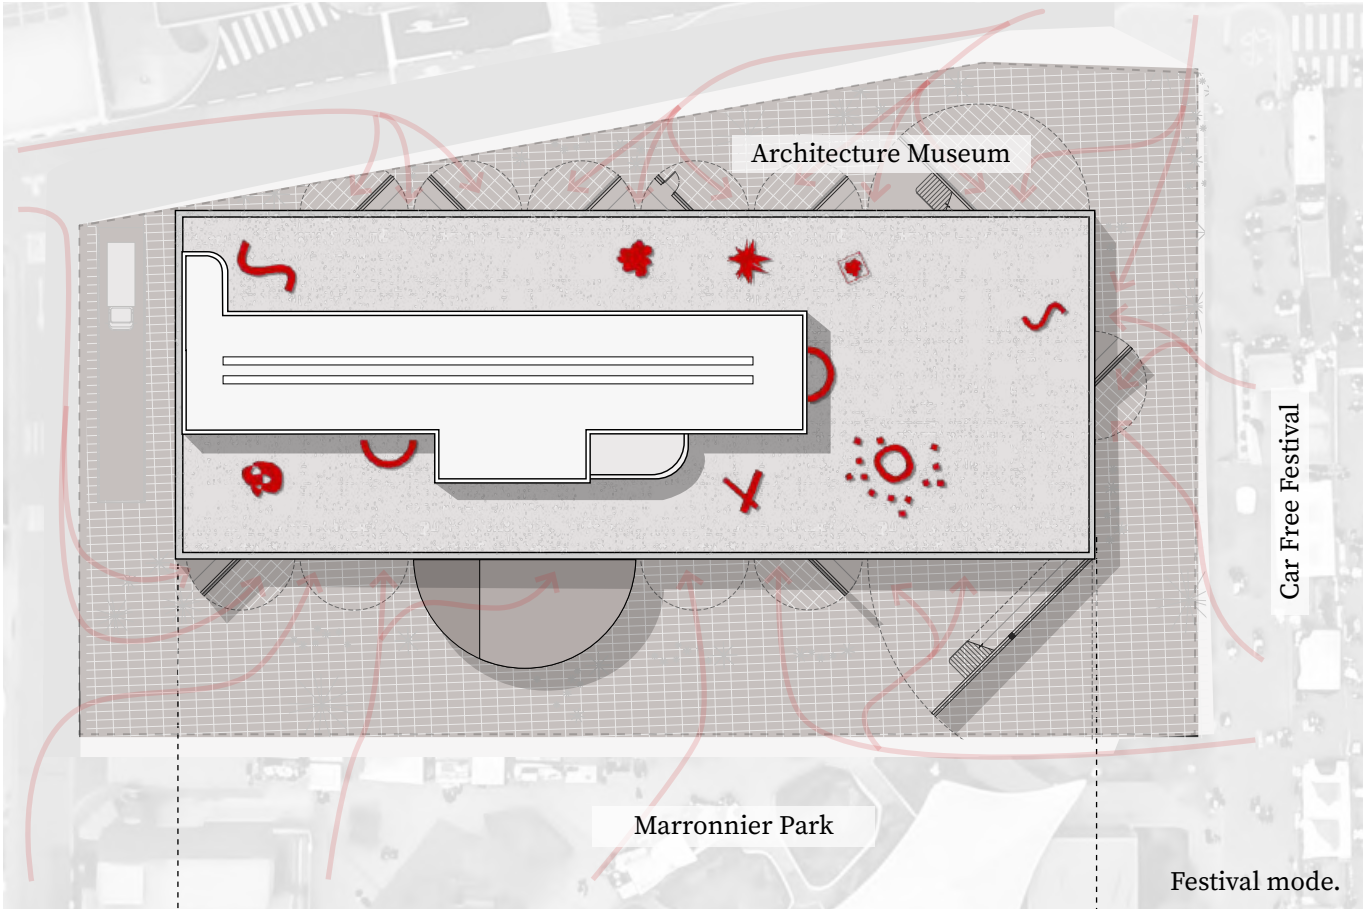

New Facade

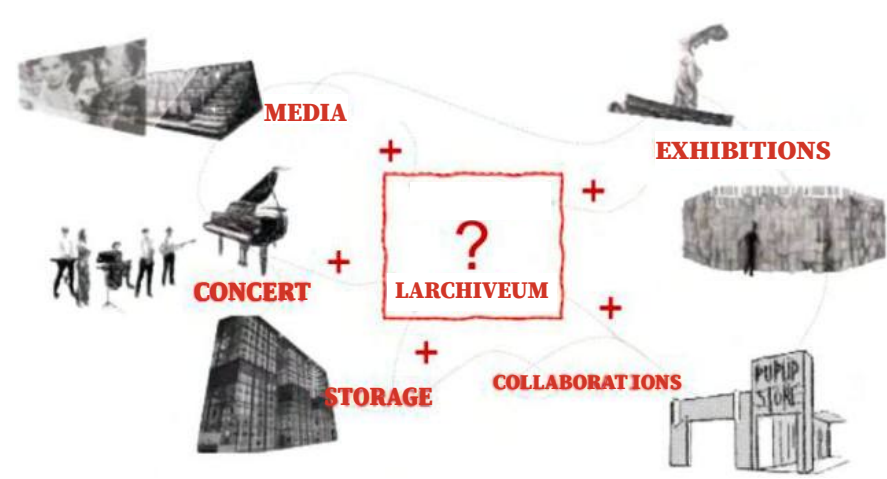

Solution. Flexible space_ Larchiveum (Library + Archive + Museum)

‘Marronnier Park’, a large gathering of people, there are several events on this place with ‘Dehakro-Road’. However, our site is definitely **disconnected with nearby moods**. We can’t even approach to this site at night except couples or ‘very’ strangers. Because there are **no lights**, no people, no chance to experience something. Connecting with the context would be the most emergent issue. At that moment, we should focus how to make people to experience the ‘architecture’ museum.

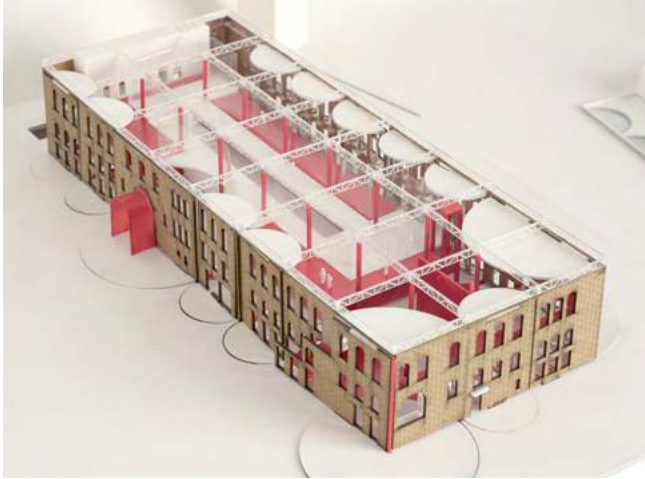


Photo. 1:200 model_ New Facade closed wall



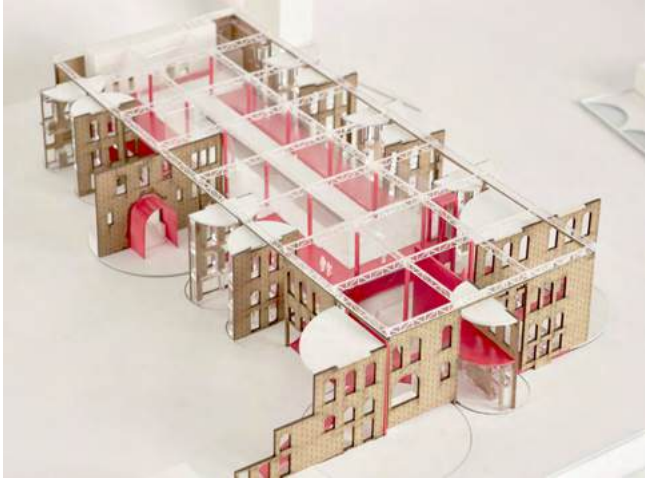


Photo. 1:200 model_ New facade opened wall


SECTION A-A'

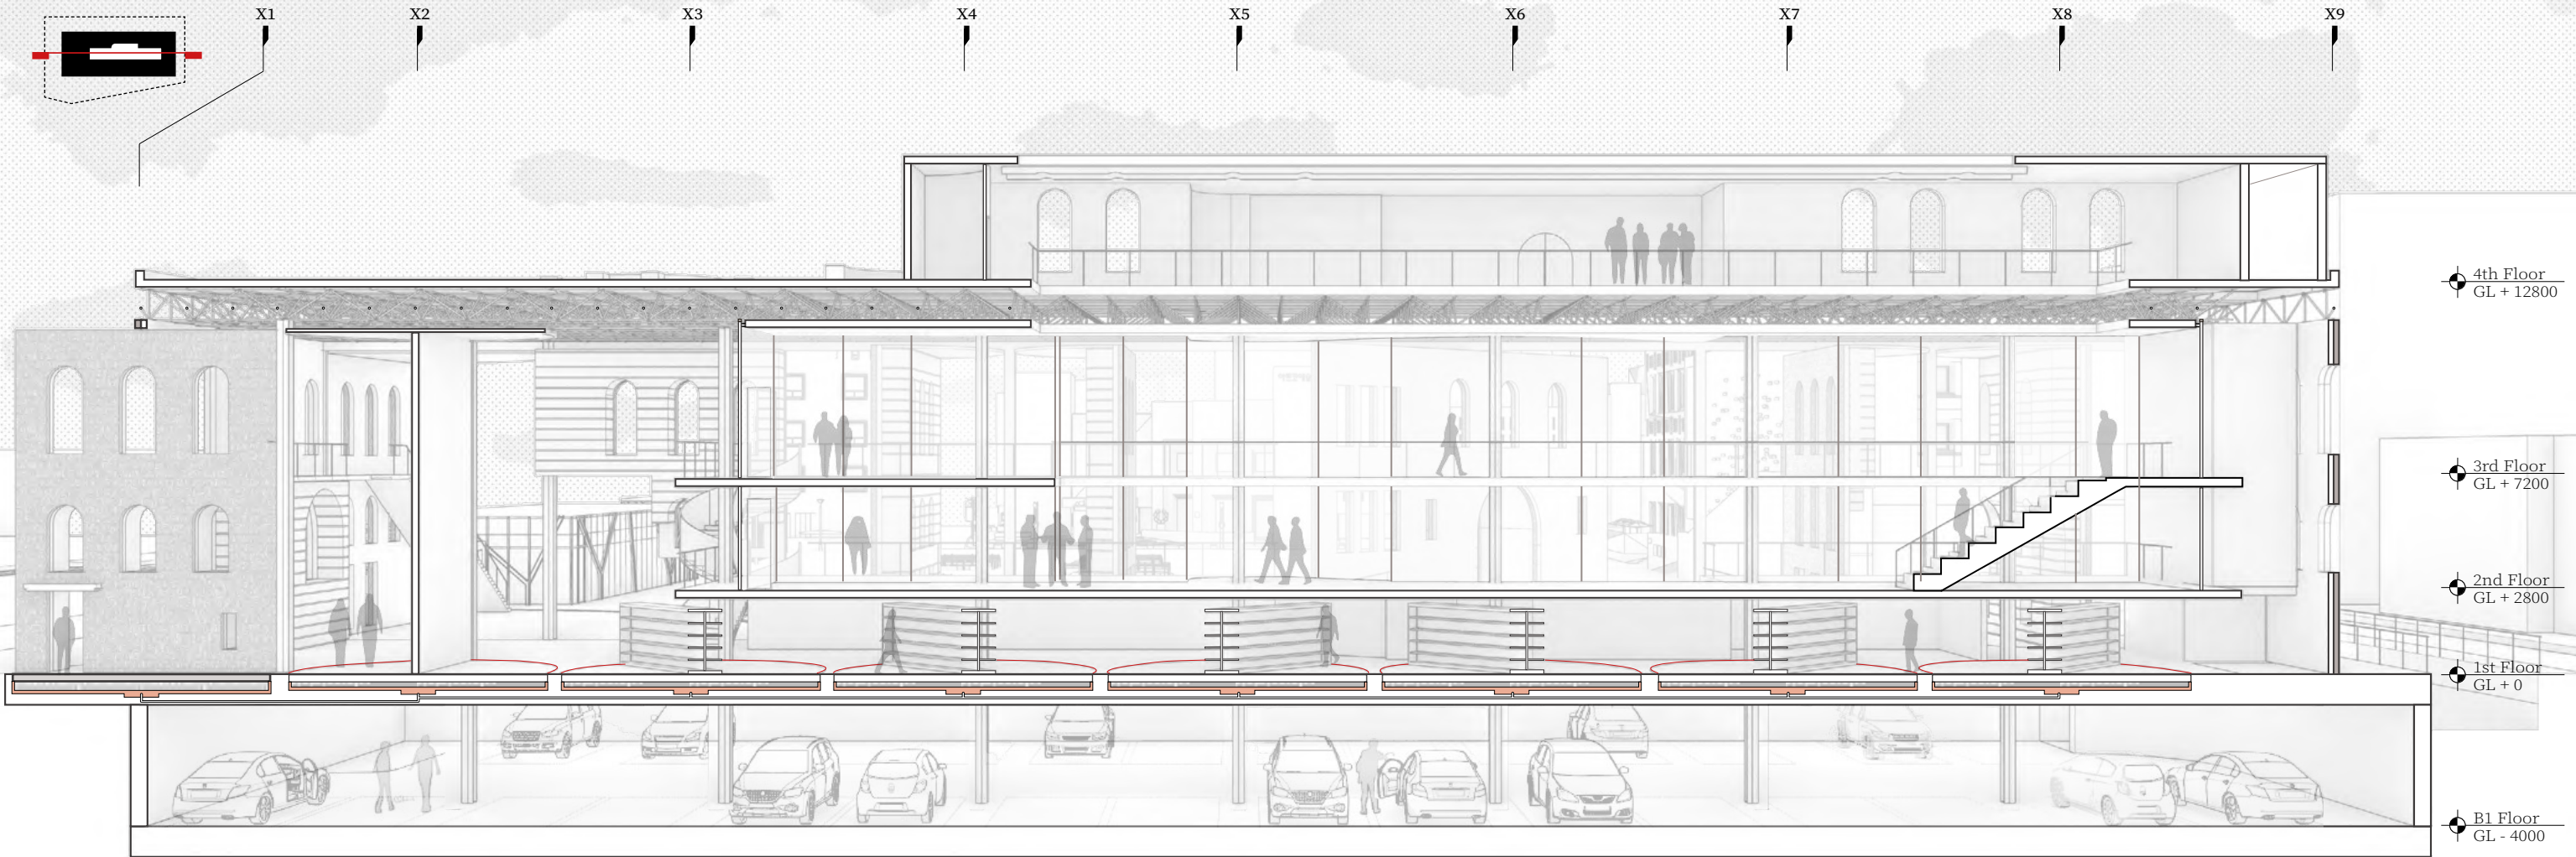

6 TYPE OF WALL UNIT : Architectural objet embedded in the wall

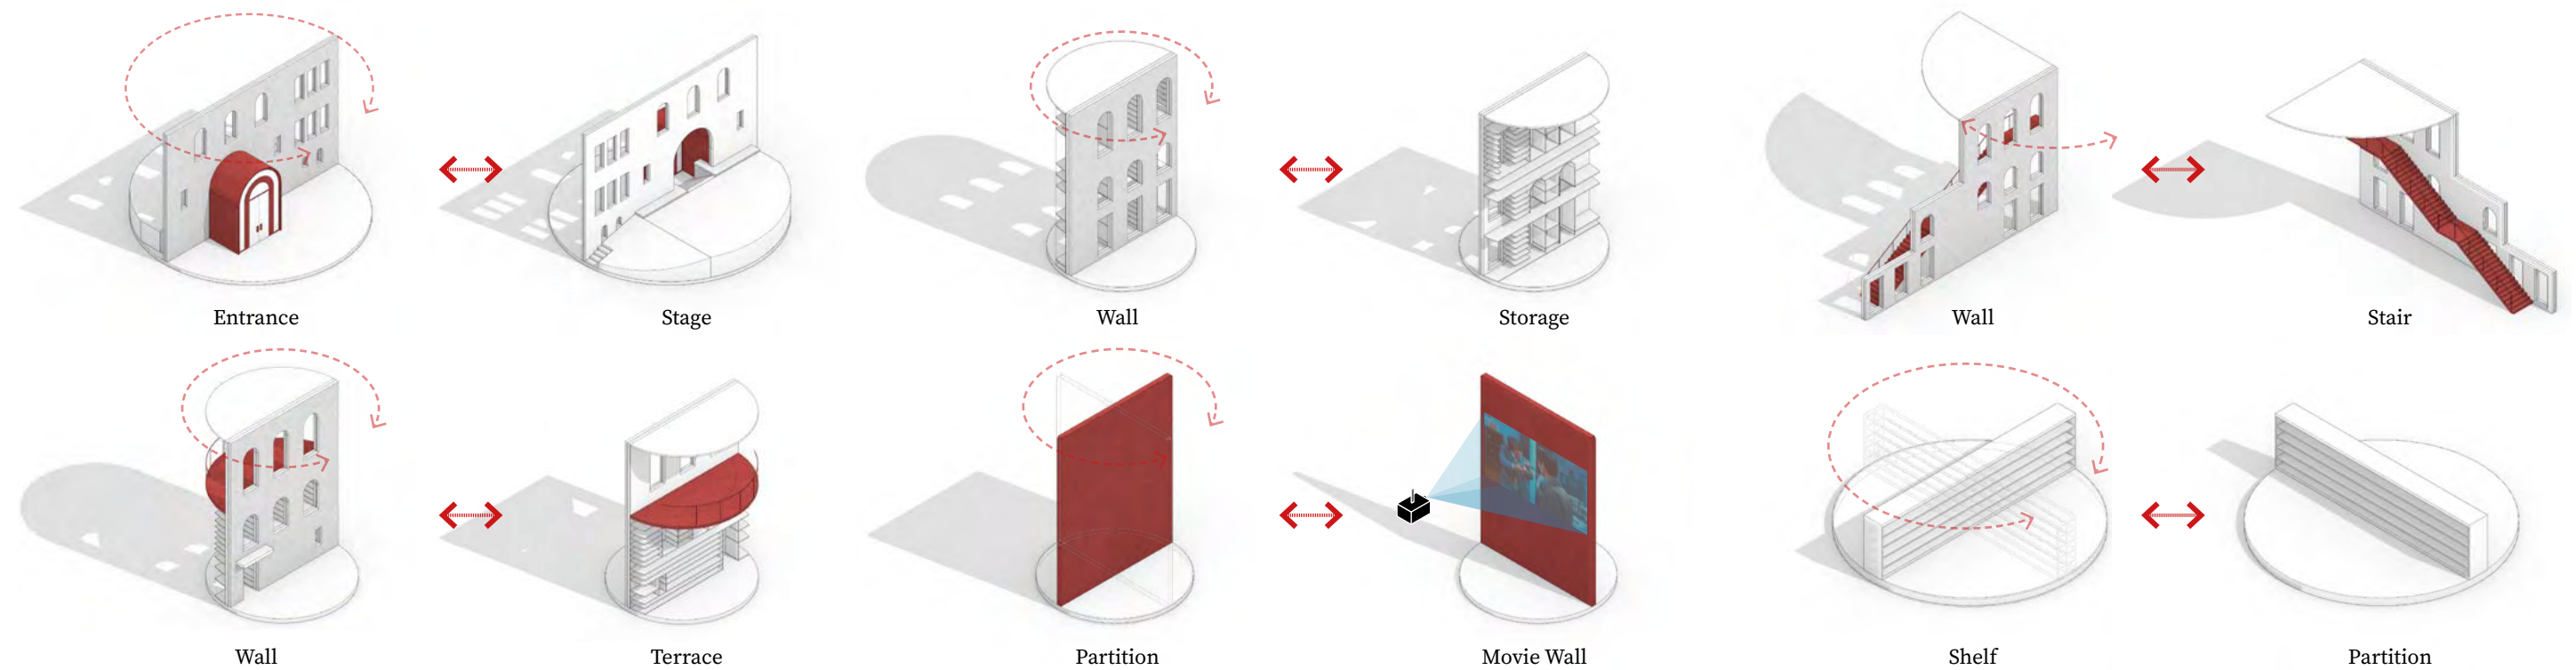

Architectural object

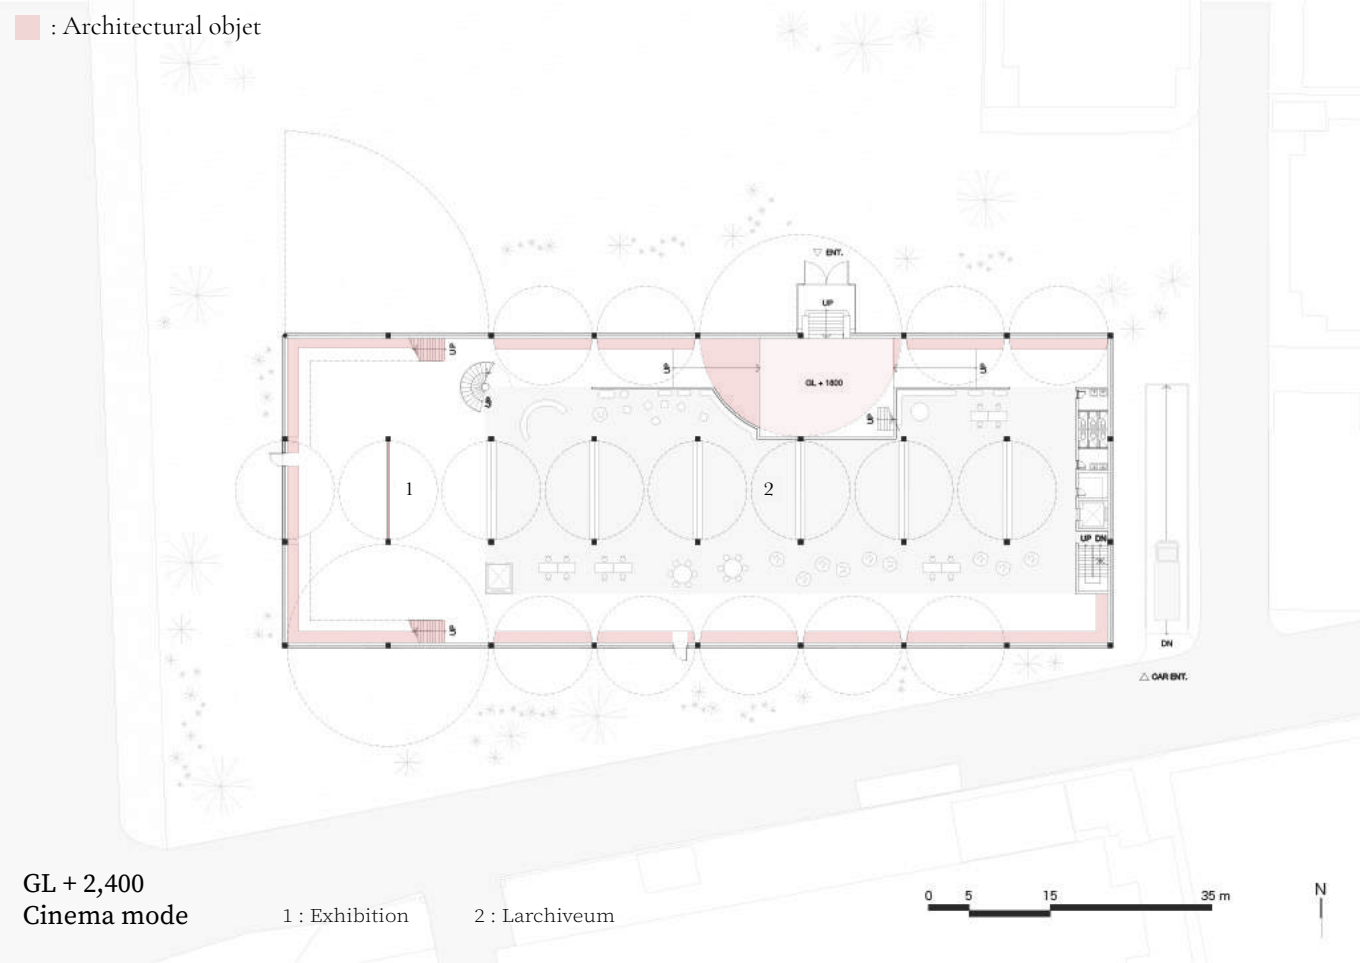

View. 2nd Floor_ Watching cinema ‘Dong-ju’ at night in cinema mode.




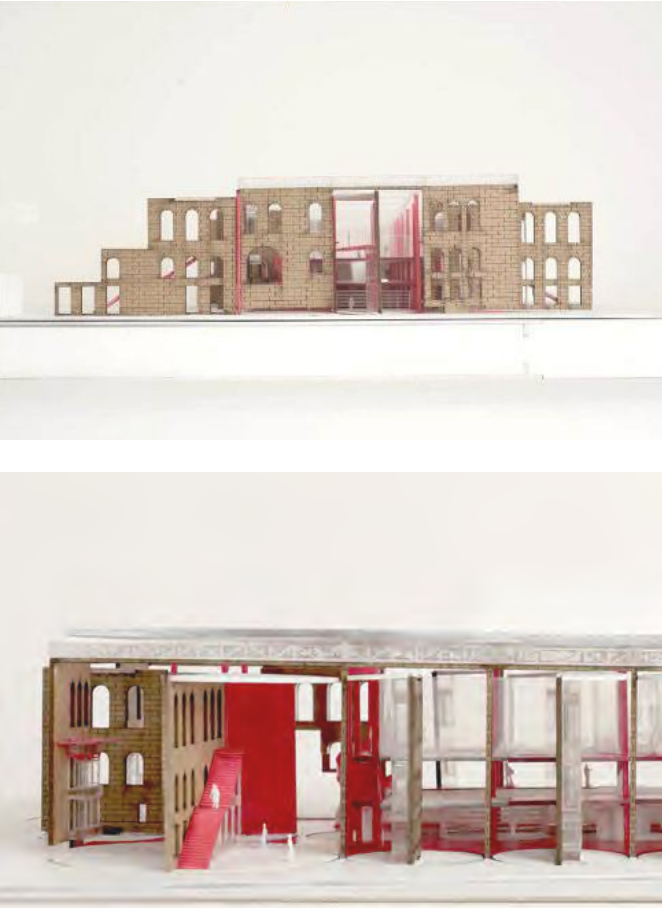


Photo. 1:200 model image

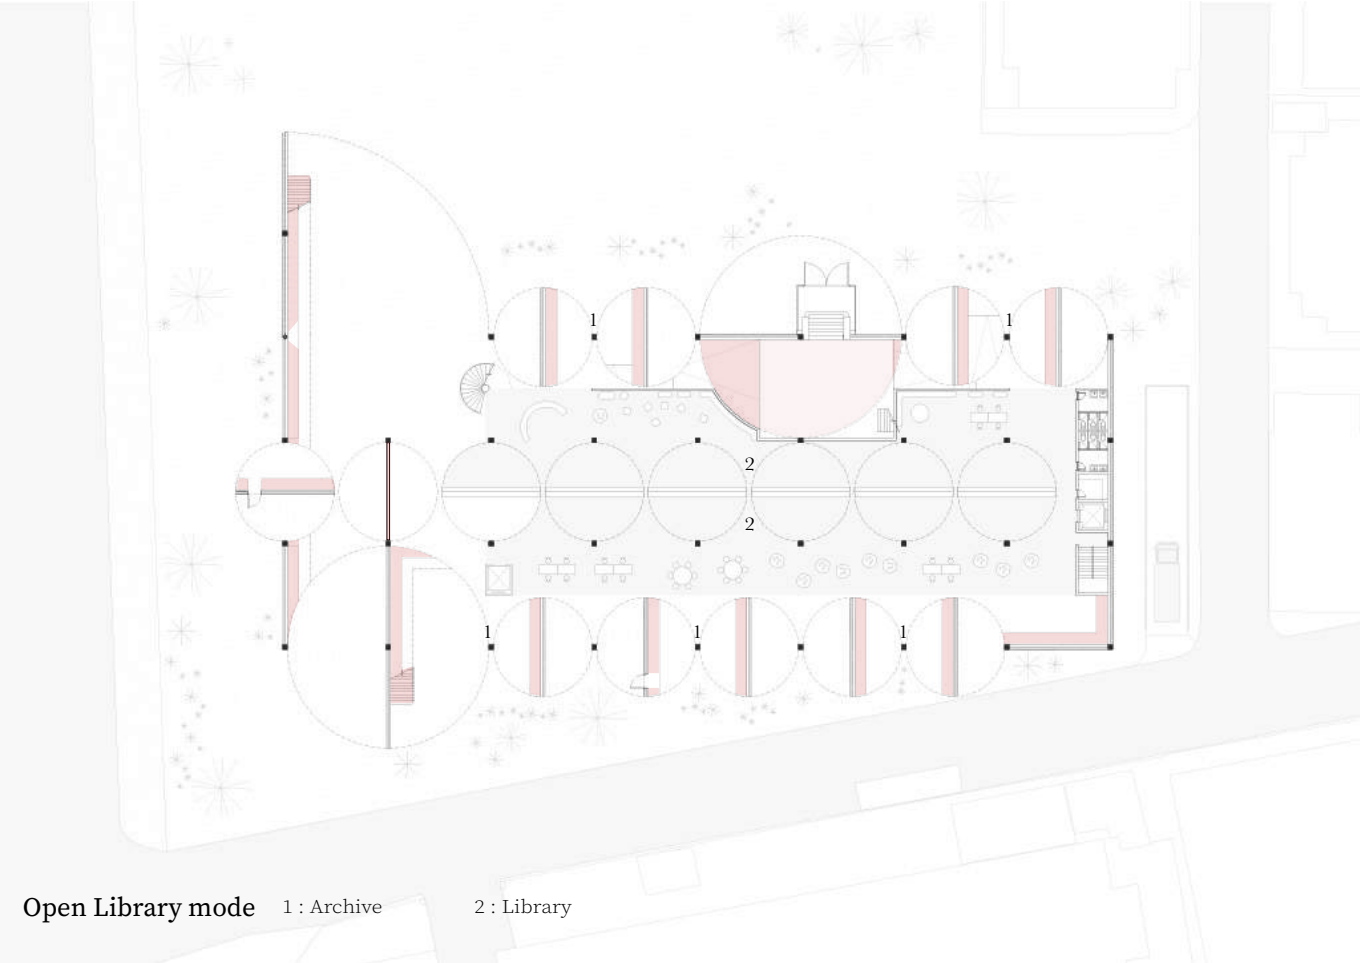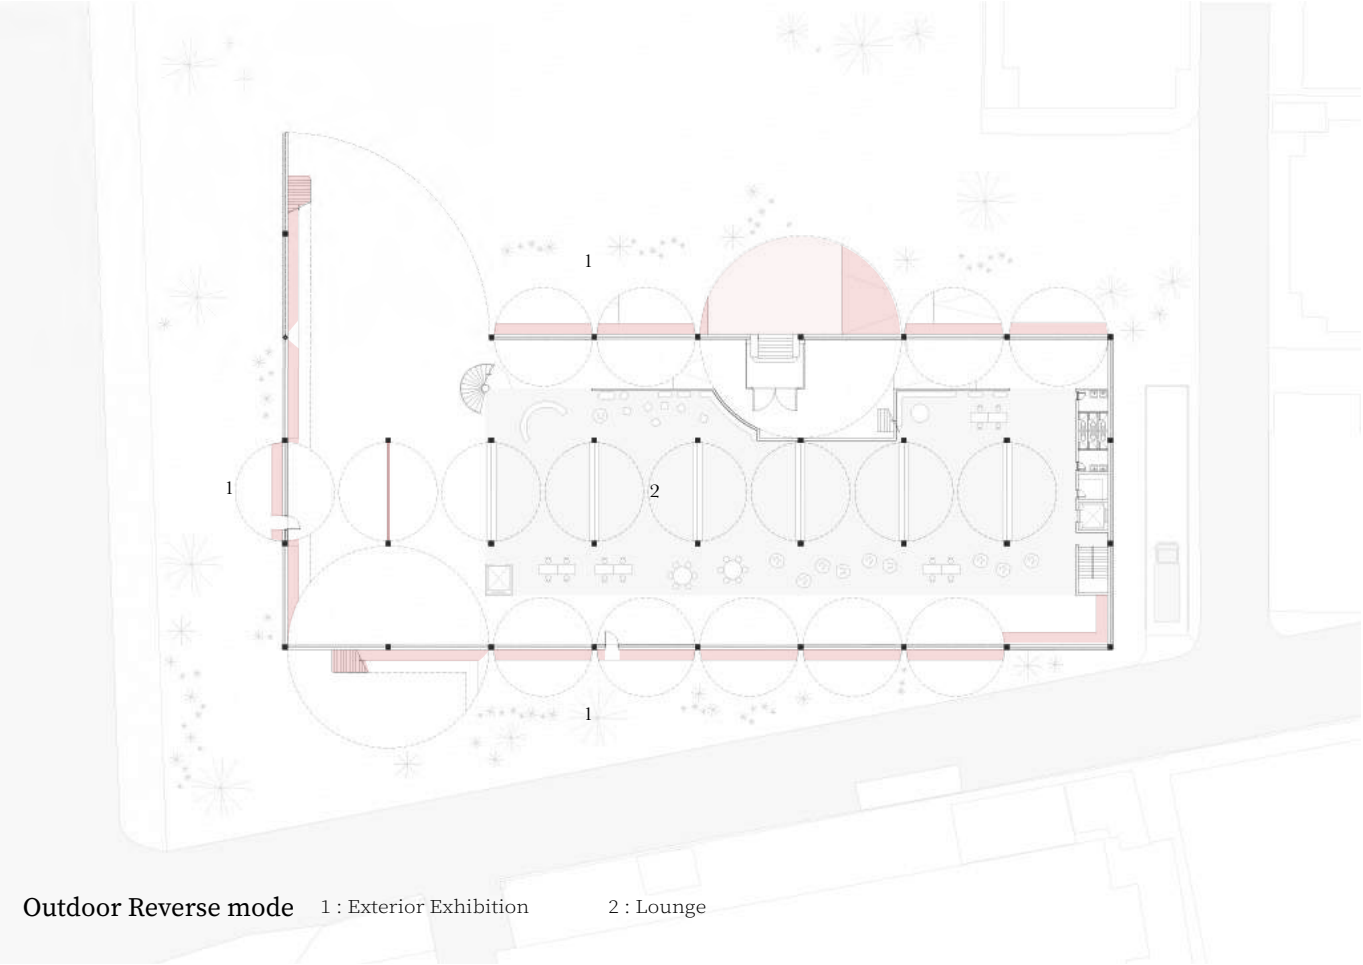

View. Outdoor entrance_ No Car Zone Festival mode

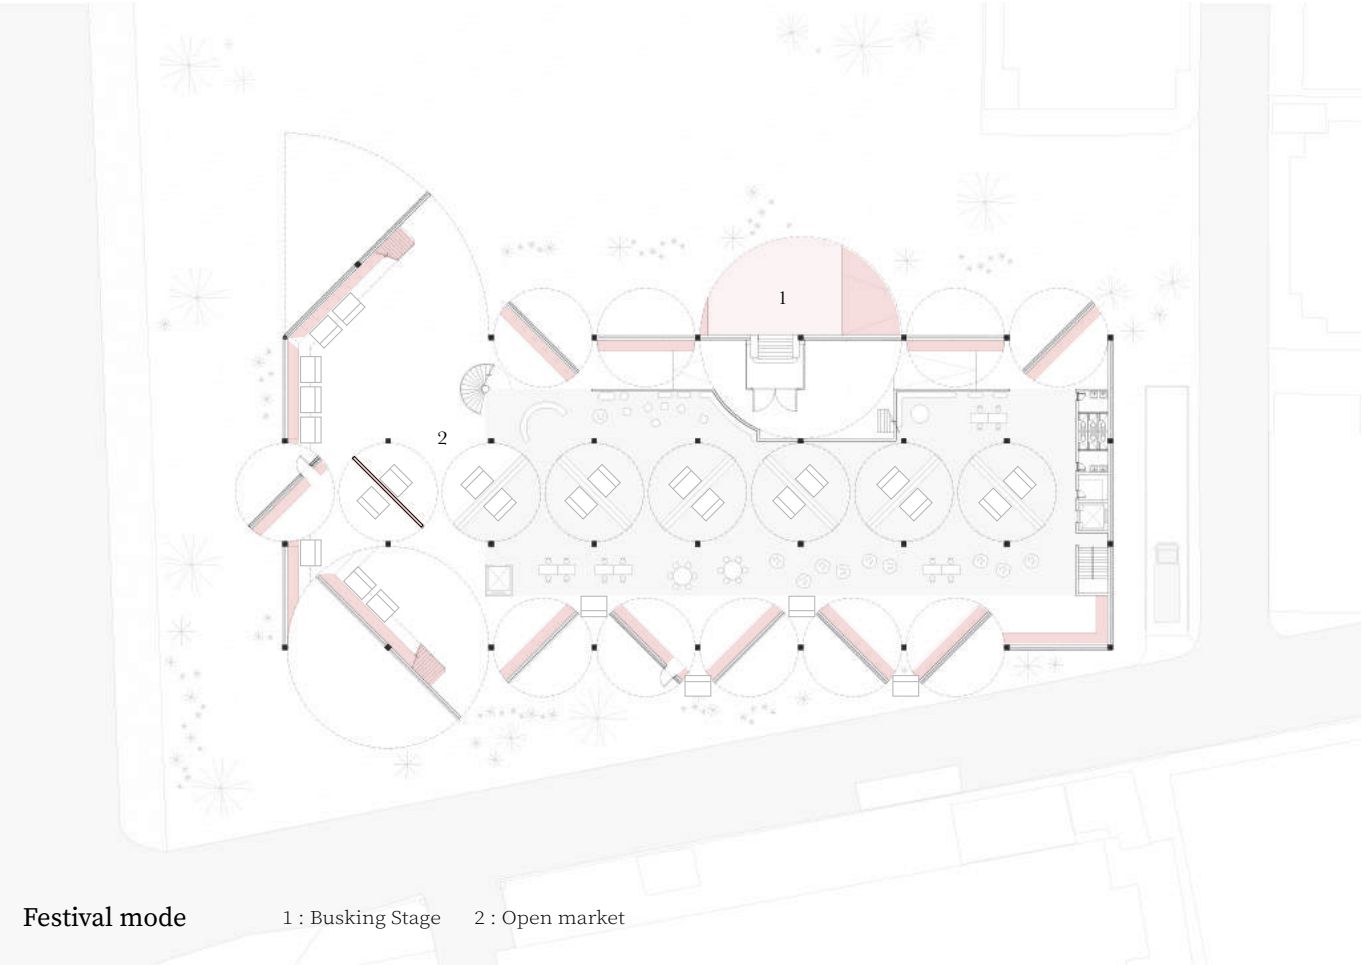

View. 3rd Floor_ Lachiveum(library + archive + museum)



Photo. 1:200 model_ Busking stage which is opposite side of the main entrance



Photo. 1:200 model_ Outdoor has been reversed with Indoor 'Terrace', 'Stairs' and 'Storage', an architectural OBJET




View 01. 1F Entrance_ Visiting an 'Art path house' on weekends

04

ART PATH HOUSE

예술家 오르樂

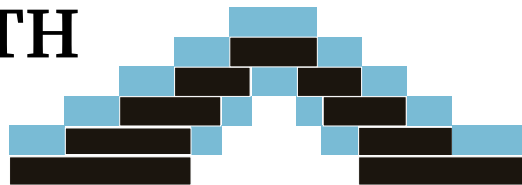


Project Information.


• Location	: Jeongreong-dong, Seoul
• Year	: 2024 - 02
• Status	: Academic study (<i>Team</i>)
• Type	: Housing Project
• Instructor	: Seongbeom Mo

Prologue.

Welcome to the ARTIST HOUSE!! We provide the opportunity to experience all kinds of art. We have 100 rooms for individual residents, including three types of modules. You can also live in the Artists' Dormitory, which offers both personal connections and inspiration for individual work. Bringing together practitioners across diverse disciplines. This is conceived as an interdisciplinary living environment that fosters both collaboration and autonomy, cultivating creative exchange within a collective residential framework.

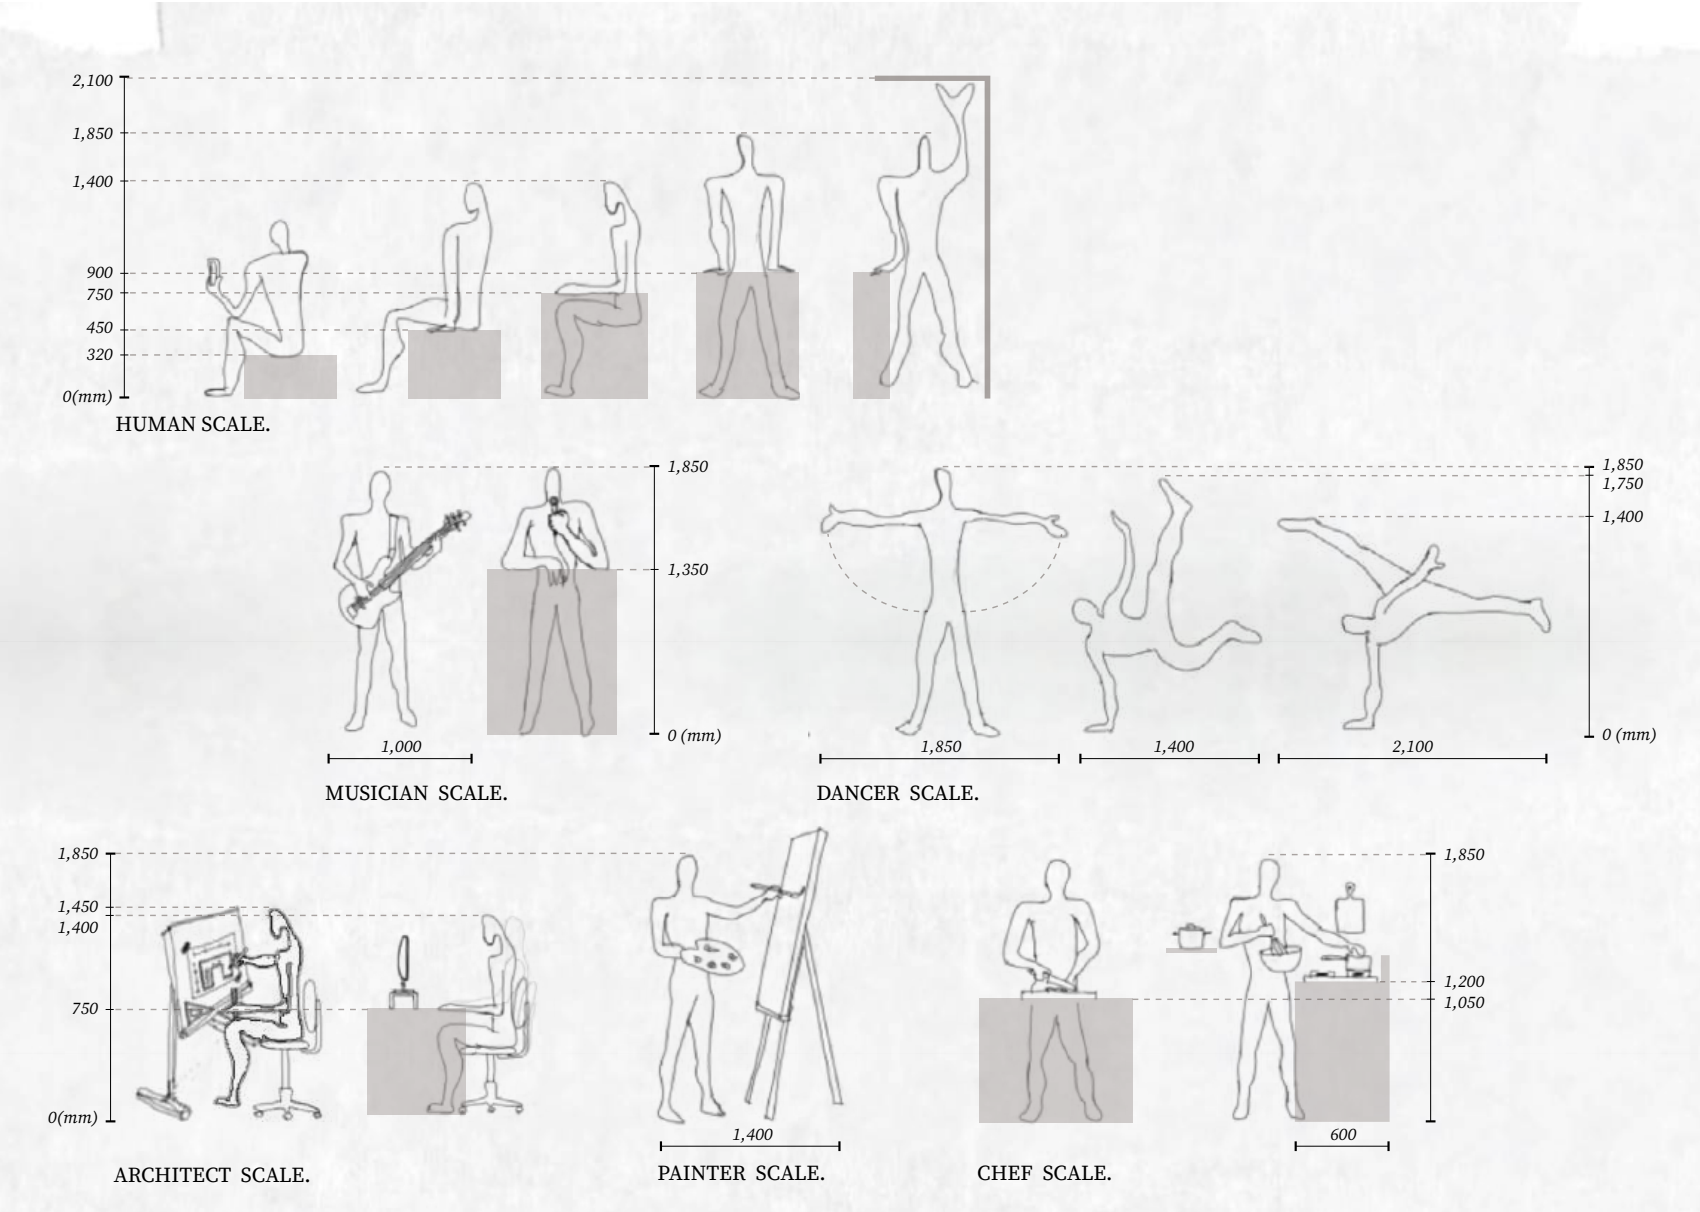

ARTIST HUMAN SCALE DRAWING.

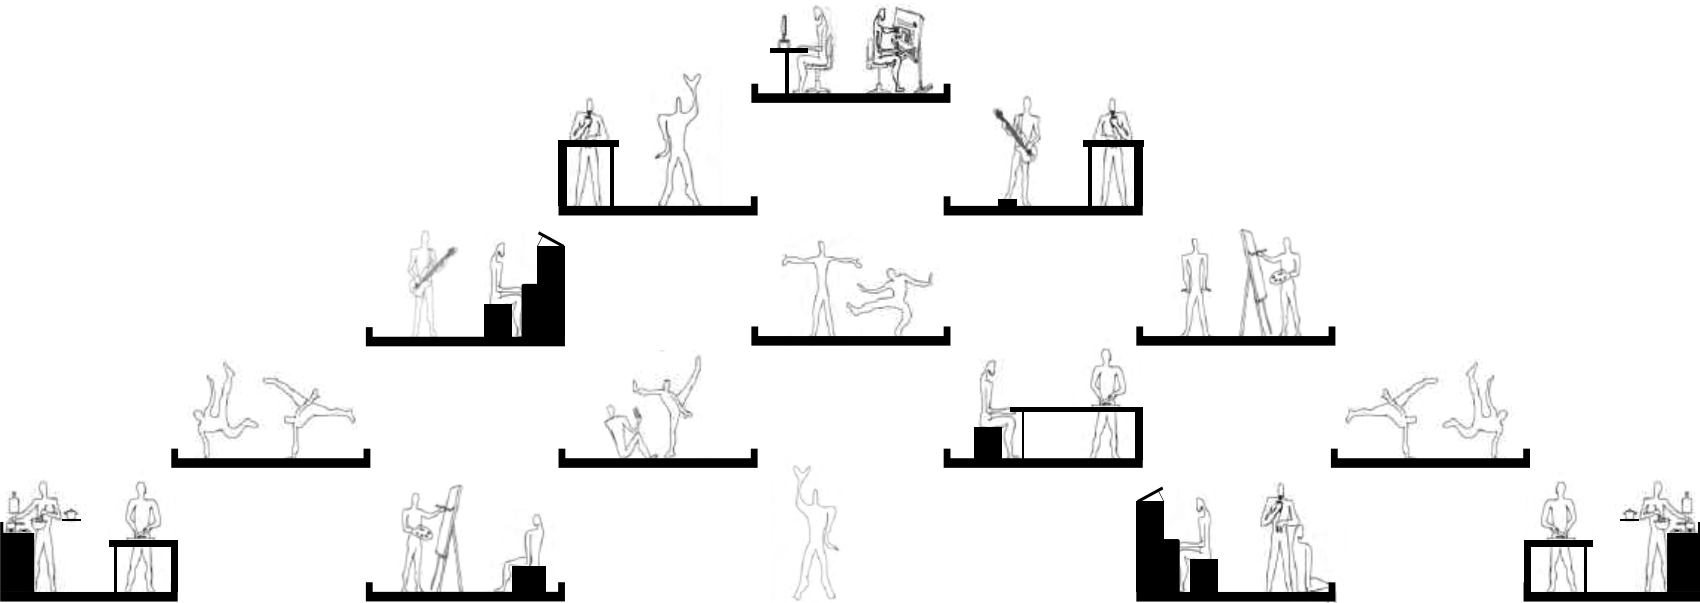

Jungneung-dong Aritist Map.

Scale 1 : 3000



Still remaining Atelier

Government's attempt

Artist's Area since 1600 s

Since the Joseon Dynasty, many literary figures—akin to today's artists—were drawn to the foot-hills of Bukhansan, where they settled and carried out their work. Following the Japanese colonial period in Korea and subsequent liberation, the area experienced rapid population growth, evolving into a clustered village community and attracting an even greater number of artists.

In modern times, many Korean artists were active in Jeongneung-dong, and although many have since left, traces of their presence remain—such as various workshops scattered throughout the area and the now-defunct government-led Jeongneung Artist Village project.

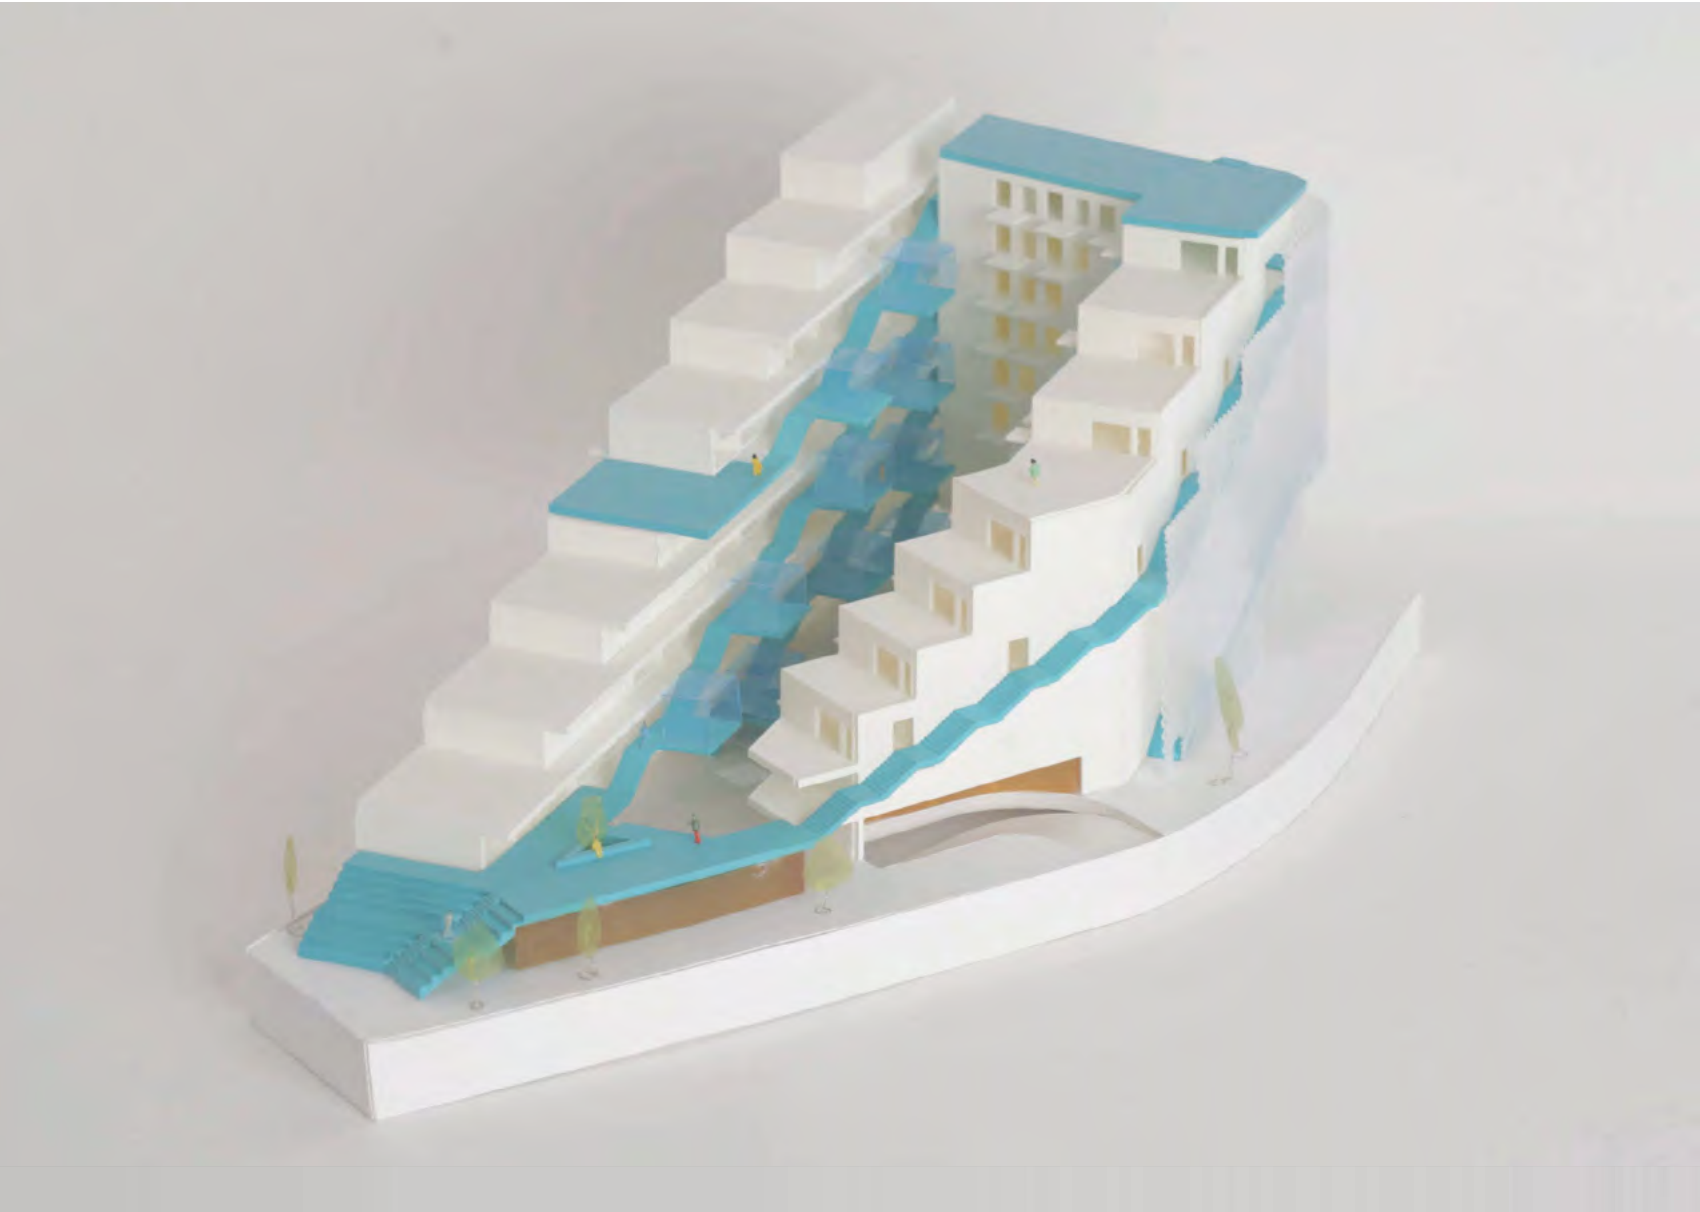



Photo. 1:200 model image_ Axonometric view



View 02. 1st Floor_ Pop-up stores for visitors




View 03. 3rd Floor stairs_ Artist selling their talent for visitors

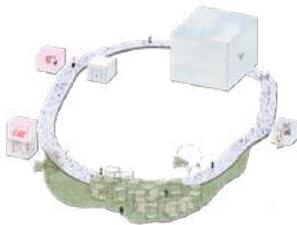

Path is one of the main space.

It encourages spontaneous encounters and shared processes, where everyday living becomes a catalyst for artistic exploration. Within this dynamic setting, individuality and community coexist, continuously shaping and enriching one another. Spaces are designed to balance privacy with chances to connect and collaborate. Here, the architecture supports everyday life while naturally encouraging creativity and interaction.

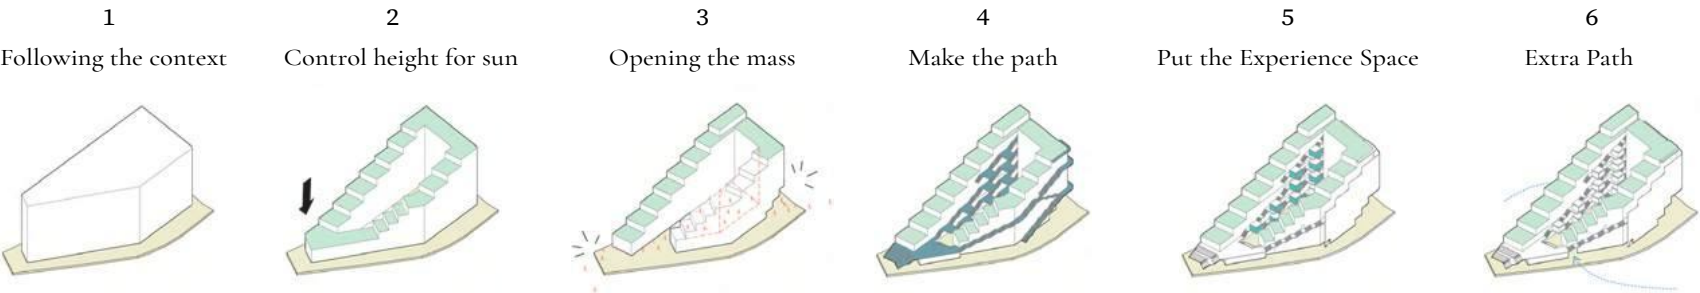


MASS PROGRESS. 1 - 2 - 3 - 4 - 5 - 6




View 04. 2nd Floor_ Take a rest and watch artists' performance



Photo. 1:200 model image_ North East Side 1

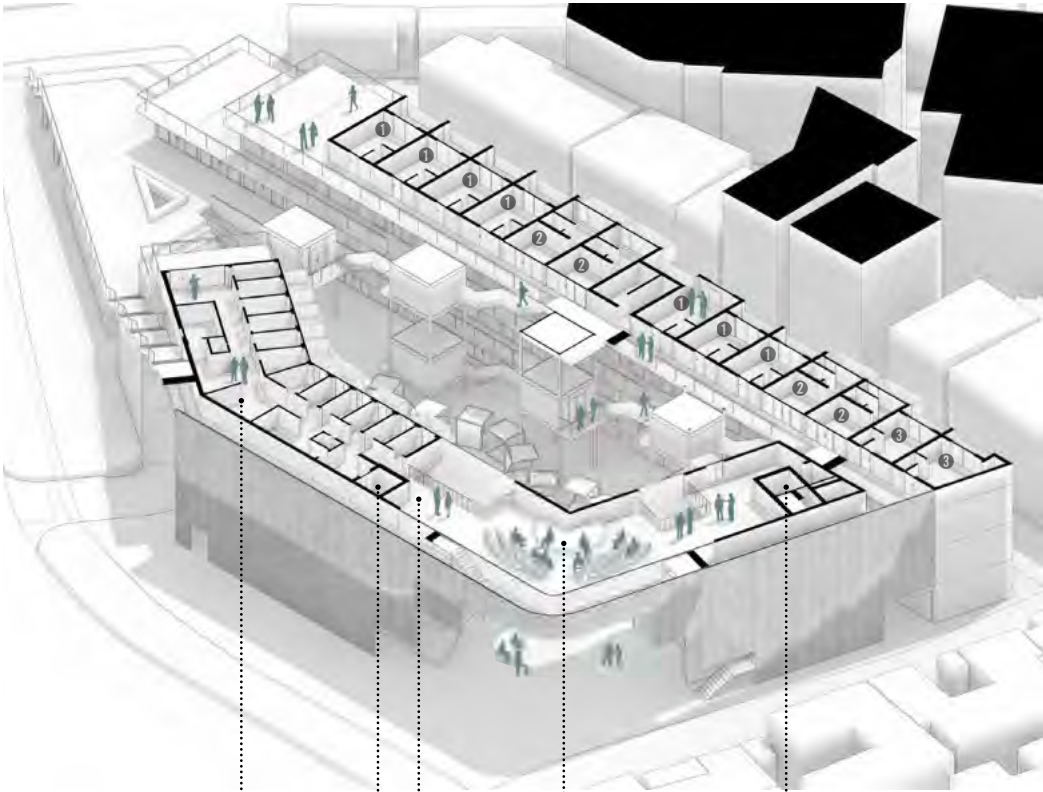

4th Floor plan. Kitchen Freight Elevator Dormitory entrance Auditorium Freight Elevator

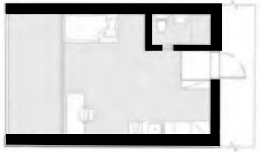

① : Life room



② : Work Life room



③ : Work Life room (2p)

Module Types.

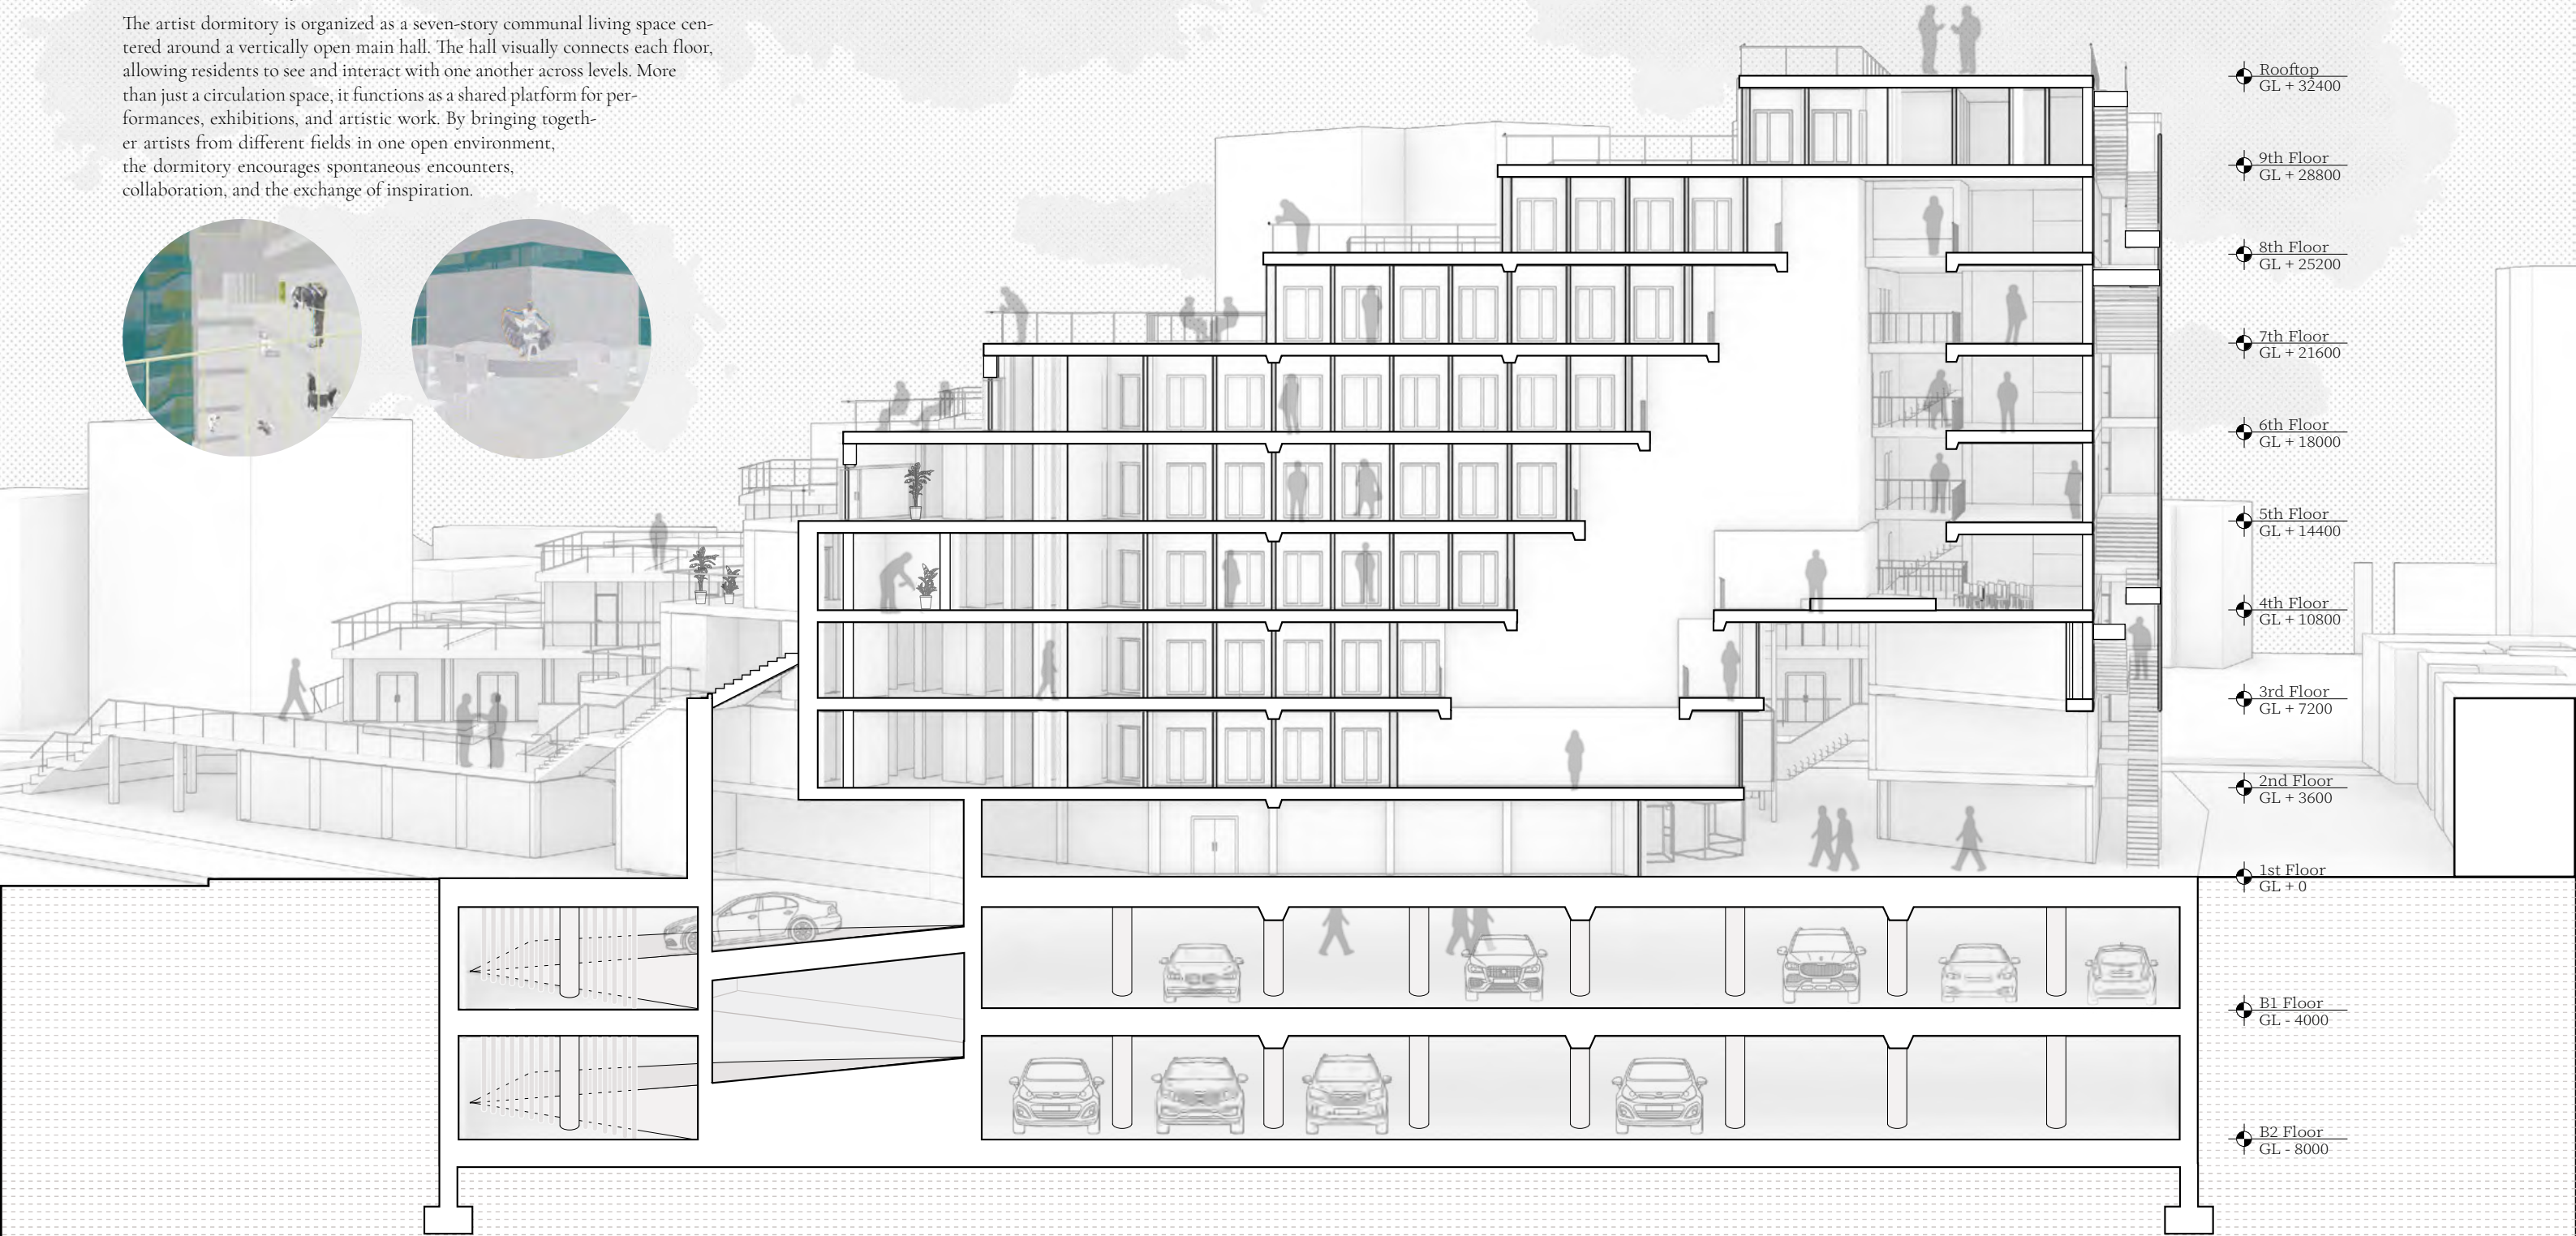


Photo. 1:200 model image_ Main entrance of the mass

X1 X2 X3 X4 X5 X6 X7


Artists' Dormitory

The artist dormitory is organized as a seven-story communal living space centered around a vertically open main hall. The hall visually connects each floor, allowing residents to see and interact with one another across levels. More than just a circulation space, it functions as a shared platform for performances, exhibitions, and artistic work. By bringing together artists from different fields in one open environment, the dormitory encourages spontaneous encounters, collaboration, and the exchange of inspiration.






05
FUTURE
CHURCH
미래교회

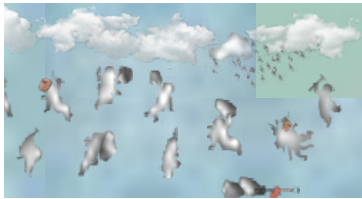


Project Information.	
• Location	: Where the small church used to be
• Year	: 2023 - 02
• Status	: Contest Bronze Prize (4th)
• Type	: Religional Park
• Instructor	: Team Project


Prologue.

A long-standing church inevitably forms deep ties with its surrounding community. For some, it is a place of worship; for others, a place of support and shared experiences—accumulating layers of memories over time. While the church has long contributed to the community as a religious facility, its sudden disappearance—despite challenges like aging and declining attendance—would be deeply felt.

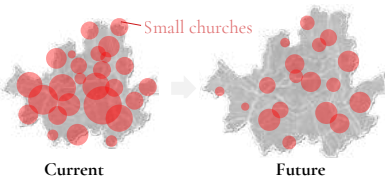


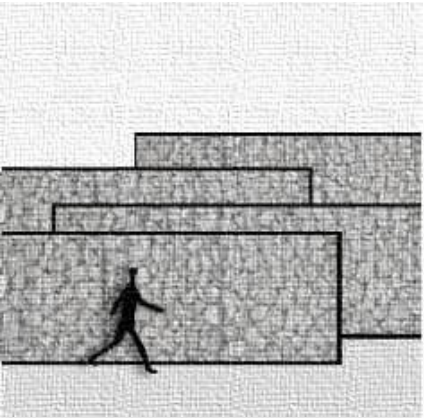

(1) Follow the Gabion wall

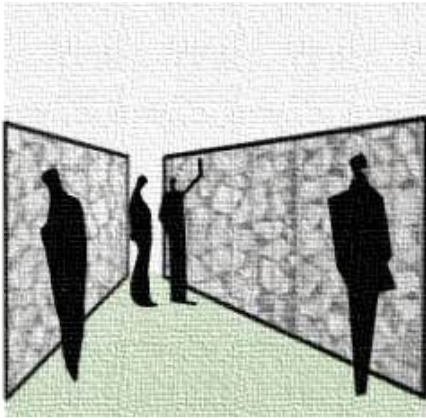


(2) Surrounded by Wall

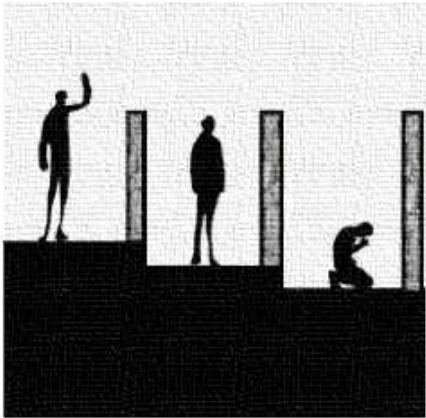


(3) Private space for each




(4) Continuas and Accessibility

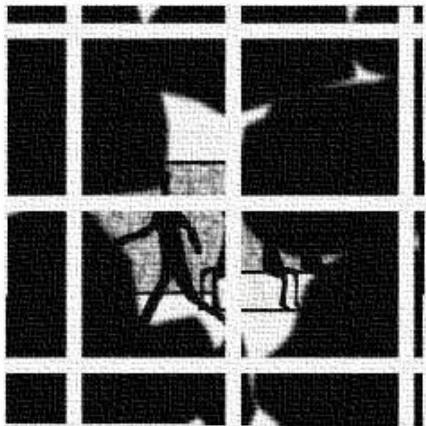


(5) View through Gabion Gap

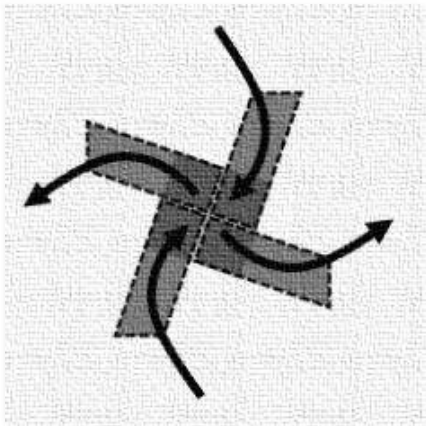


(6) Opened Sanctorum

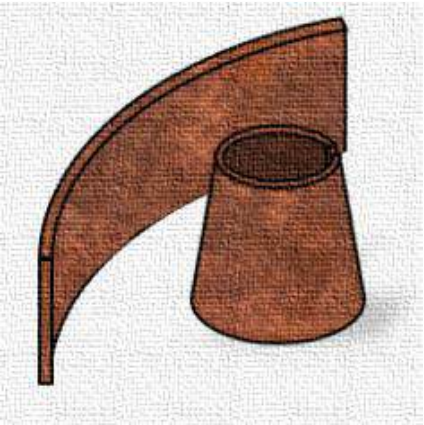


(7) Corten Steel Statue

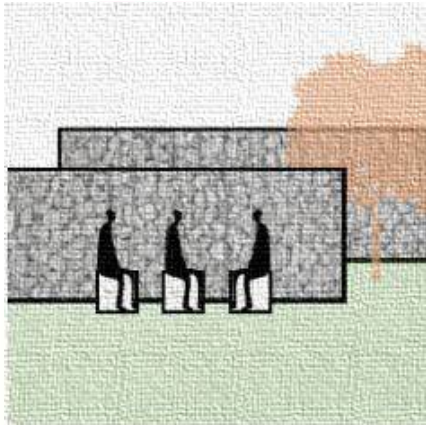

(8) Space for Community

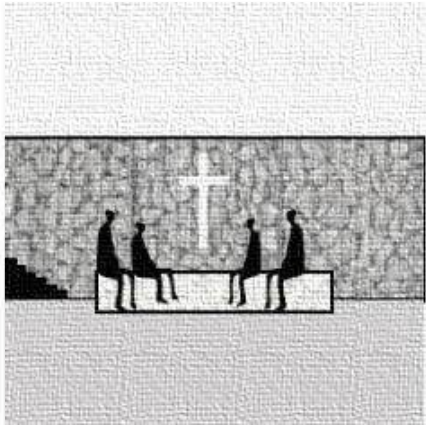

(9) Space for worship

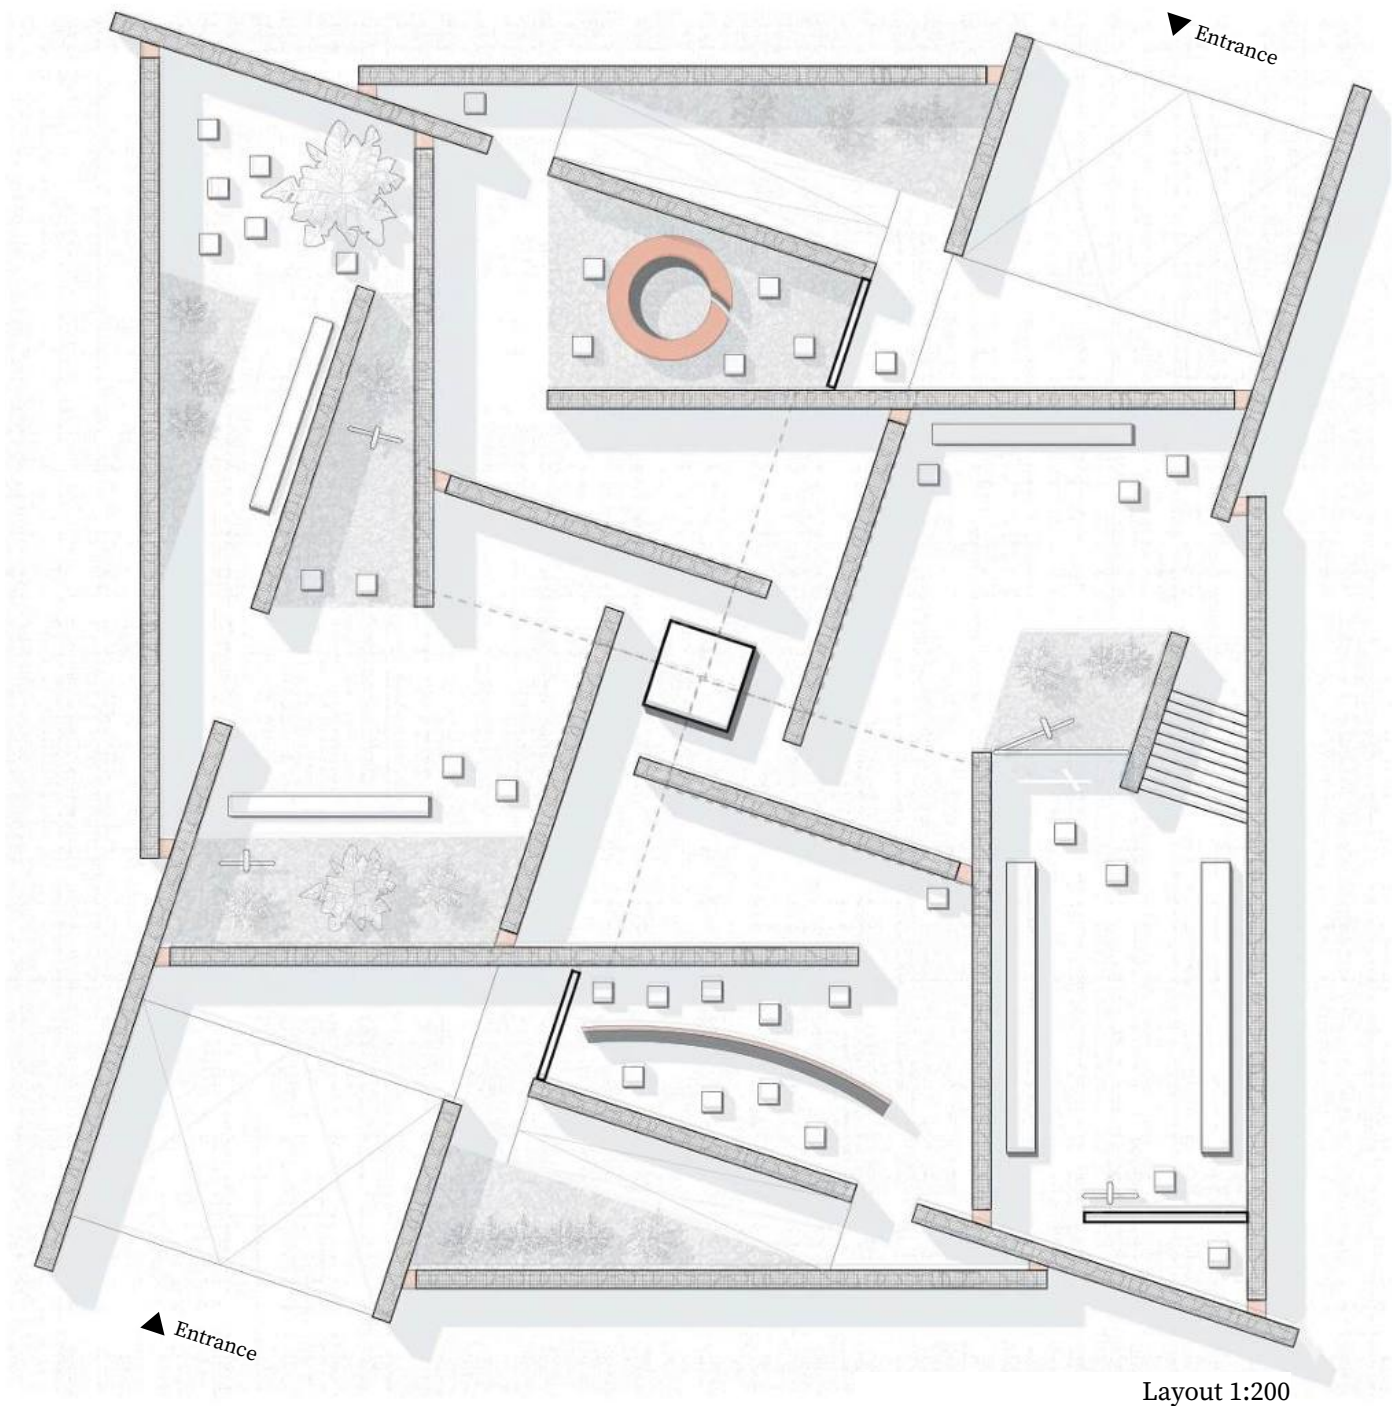

Layout 1:200



View. A man in the Oratory



View. Middle of the Park

This project respects the existing church and its relationships, reimagining it as an open park that continues to serve the community. In this sense, it becomes a new form of open sanctuary that preserves the essence of the original place.



View. Space for worship or rest



Photo. 1:50 model image

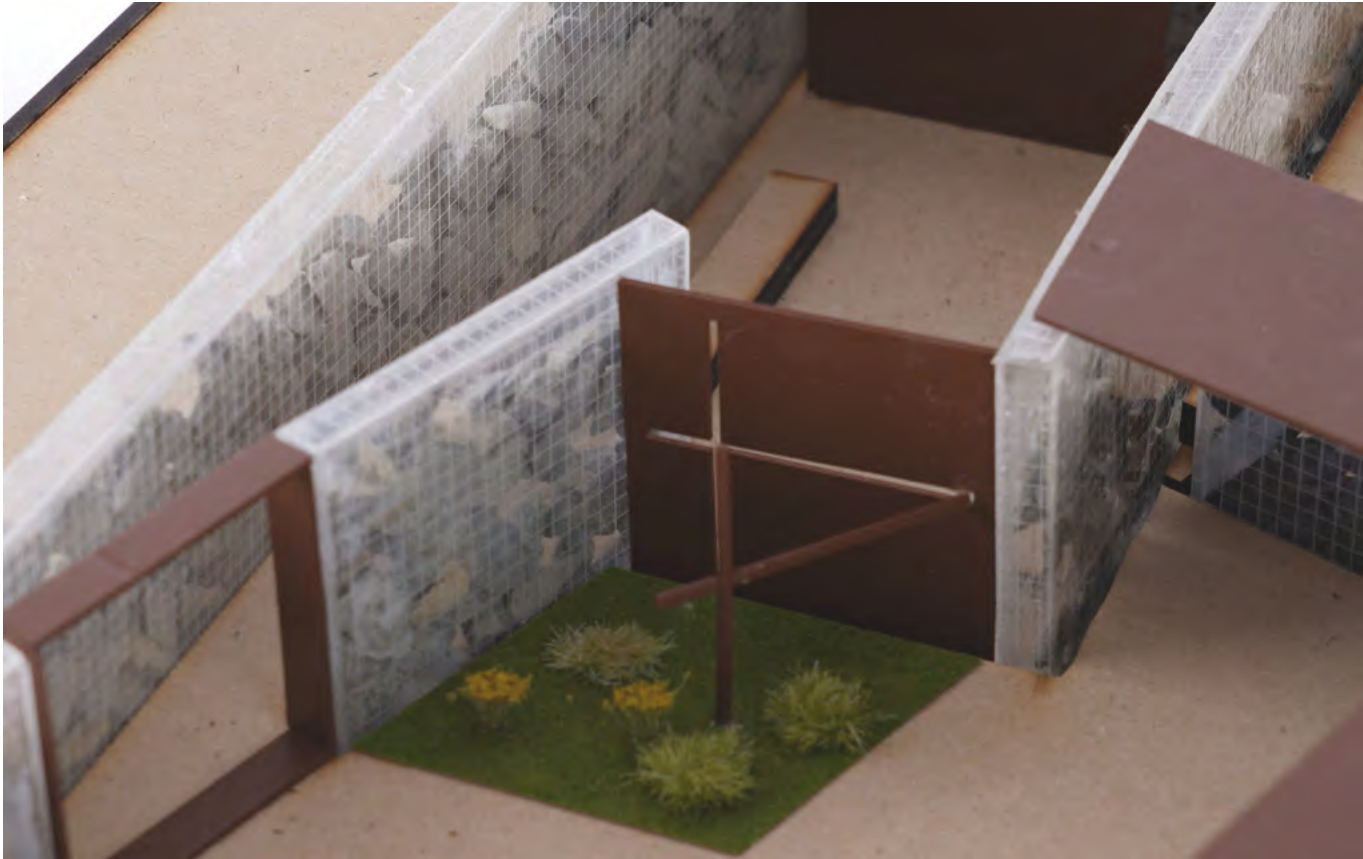


Photo. 1:50 model image_ Before getting in to the worship space



Photo. 1:50 model image_ Oratory : prayer space



Photo. Pavilion in the Seoul Square

06 SIMBIONT :LIVE LIFE

숨터 : 공생



Project Information.

- Location : Seoul City Hall Square
- Year : 2025 - summer
- Status : Excellence Prize(3rd), Citizen Prize
- Type : Pavilion
- Instructor : Team Project

Prologue.

How does nature coexist?
How can Human coexist with nature?

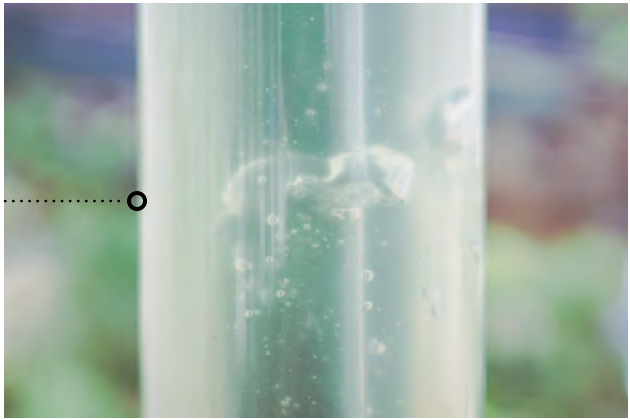


Photo. H2O Bubble in the unit

In this era, humans tend to see nature only as a ‘resource.’ However, the pavilion ‘Symbiont’ models this ecological operation, proposing a space of symbiosis by imitating nature’s cyclical systems, the ‘Bromeliad’. It forms micro-ecosystem in its water tank between leaves. We spatializes a system of coexistence, allowing visitors to shift from observers to participants, from consumers to resource providers.



Photo. Pavilion under the sky

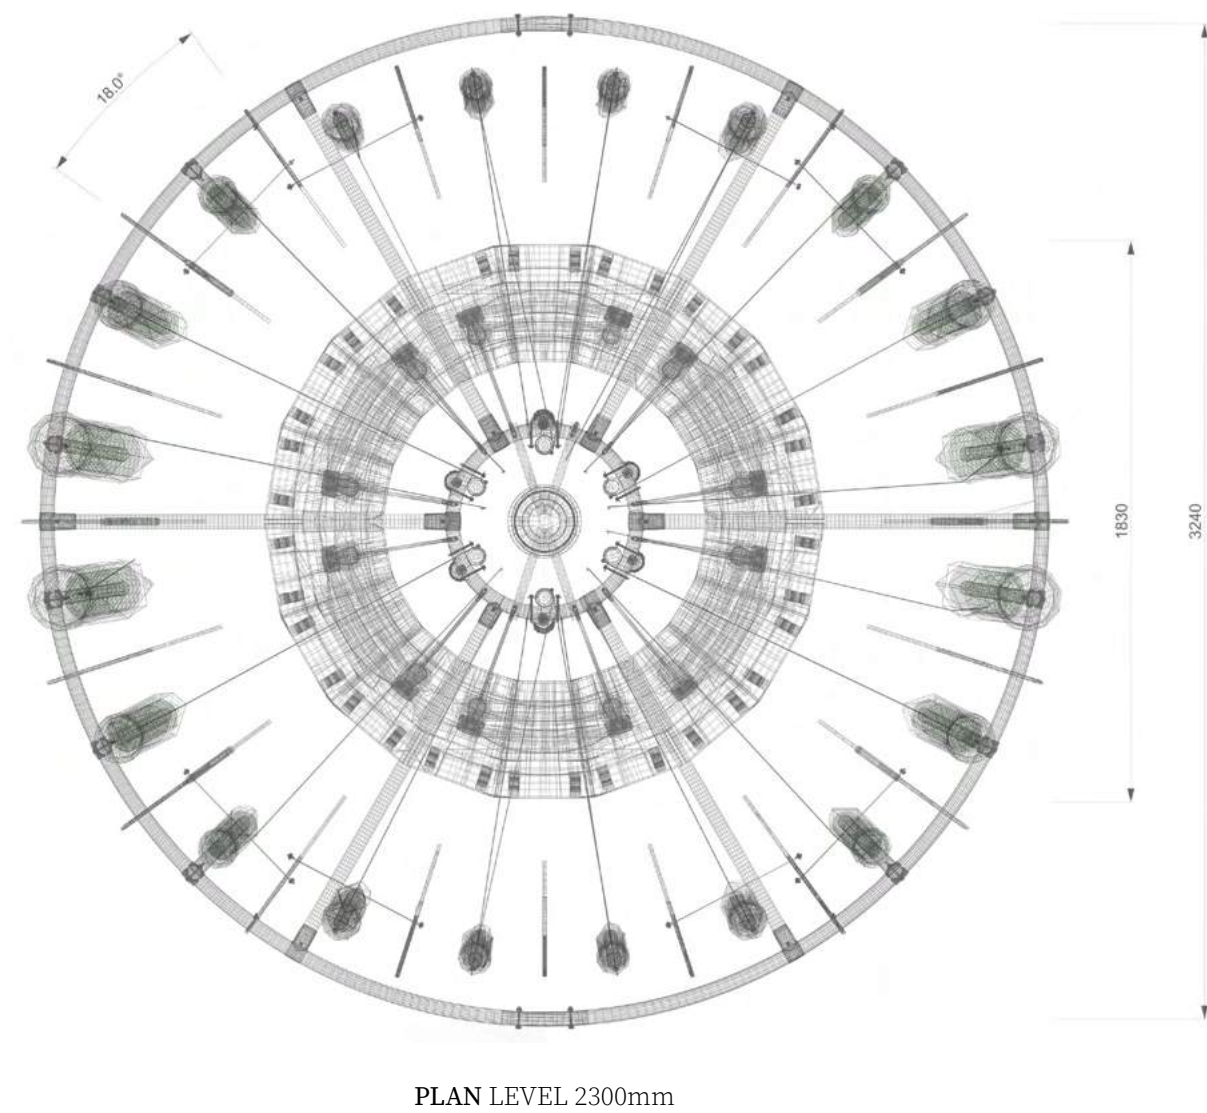
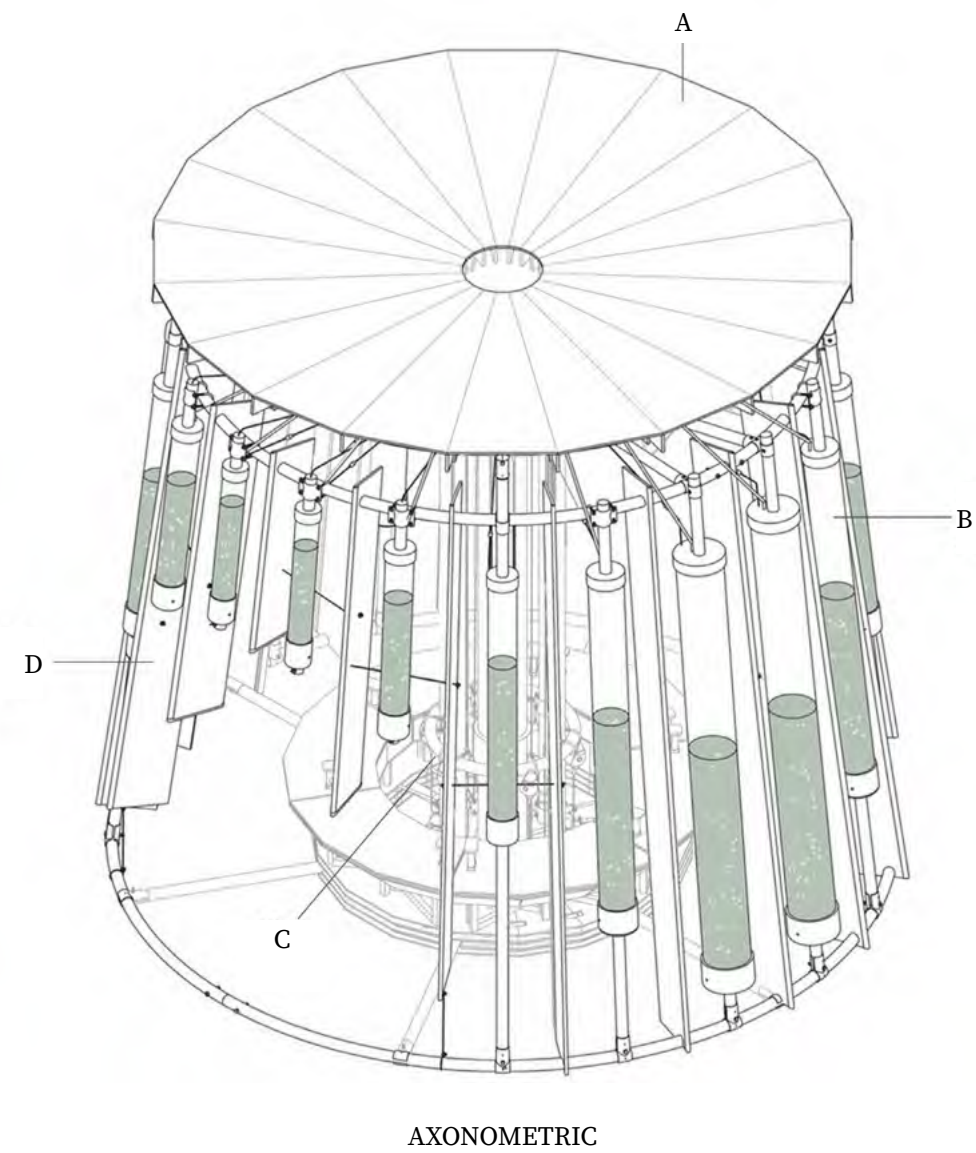
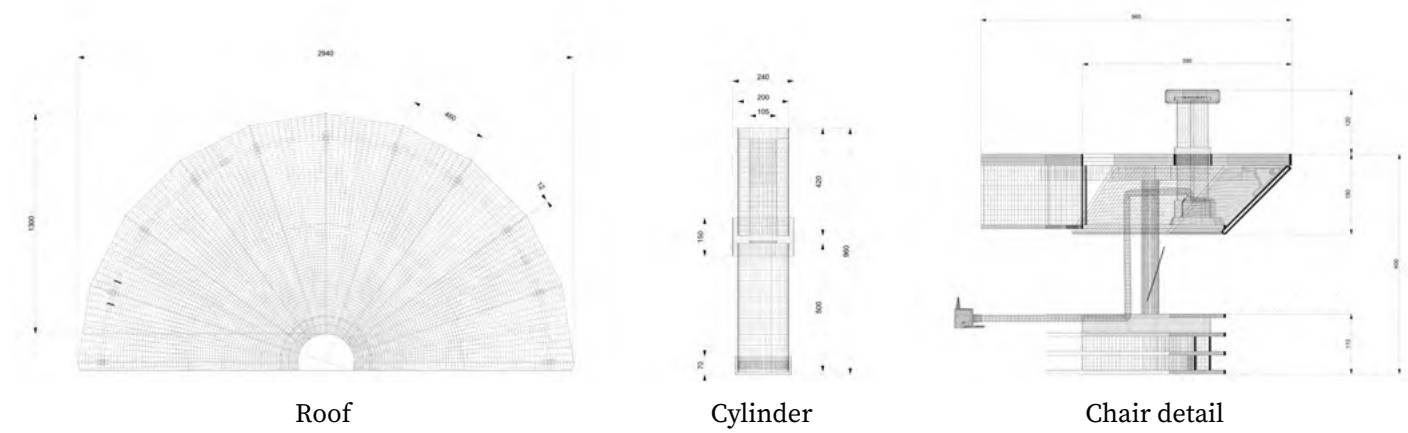
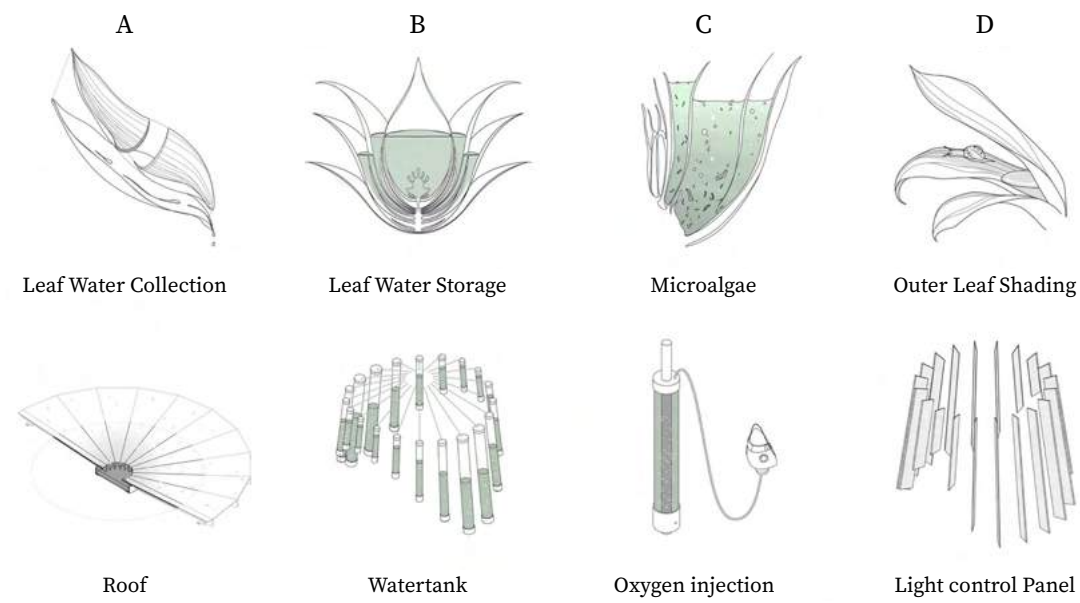




Photo. 1:1 pavilion image_ Entrance view



Photo. 1:1 pavilion image_ Seat detail : Recycled wood



Photo. 1:1 pavilion image_ Roof detail : Recycled wood



Photo. 1:1 pavilion image_ Structure connection detail : T-clamp



Photo. 1:1 pavilion image_ Polycarbonate wall detail : 3D Printed